


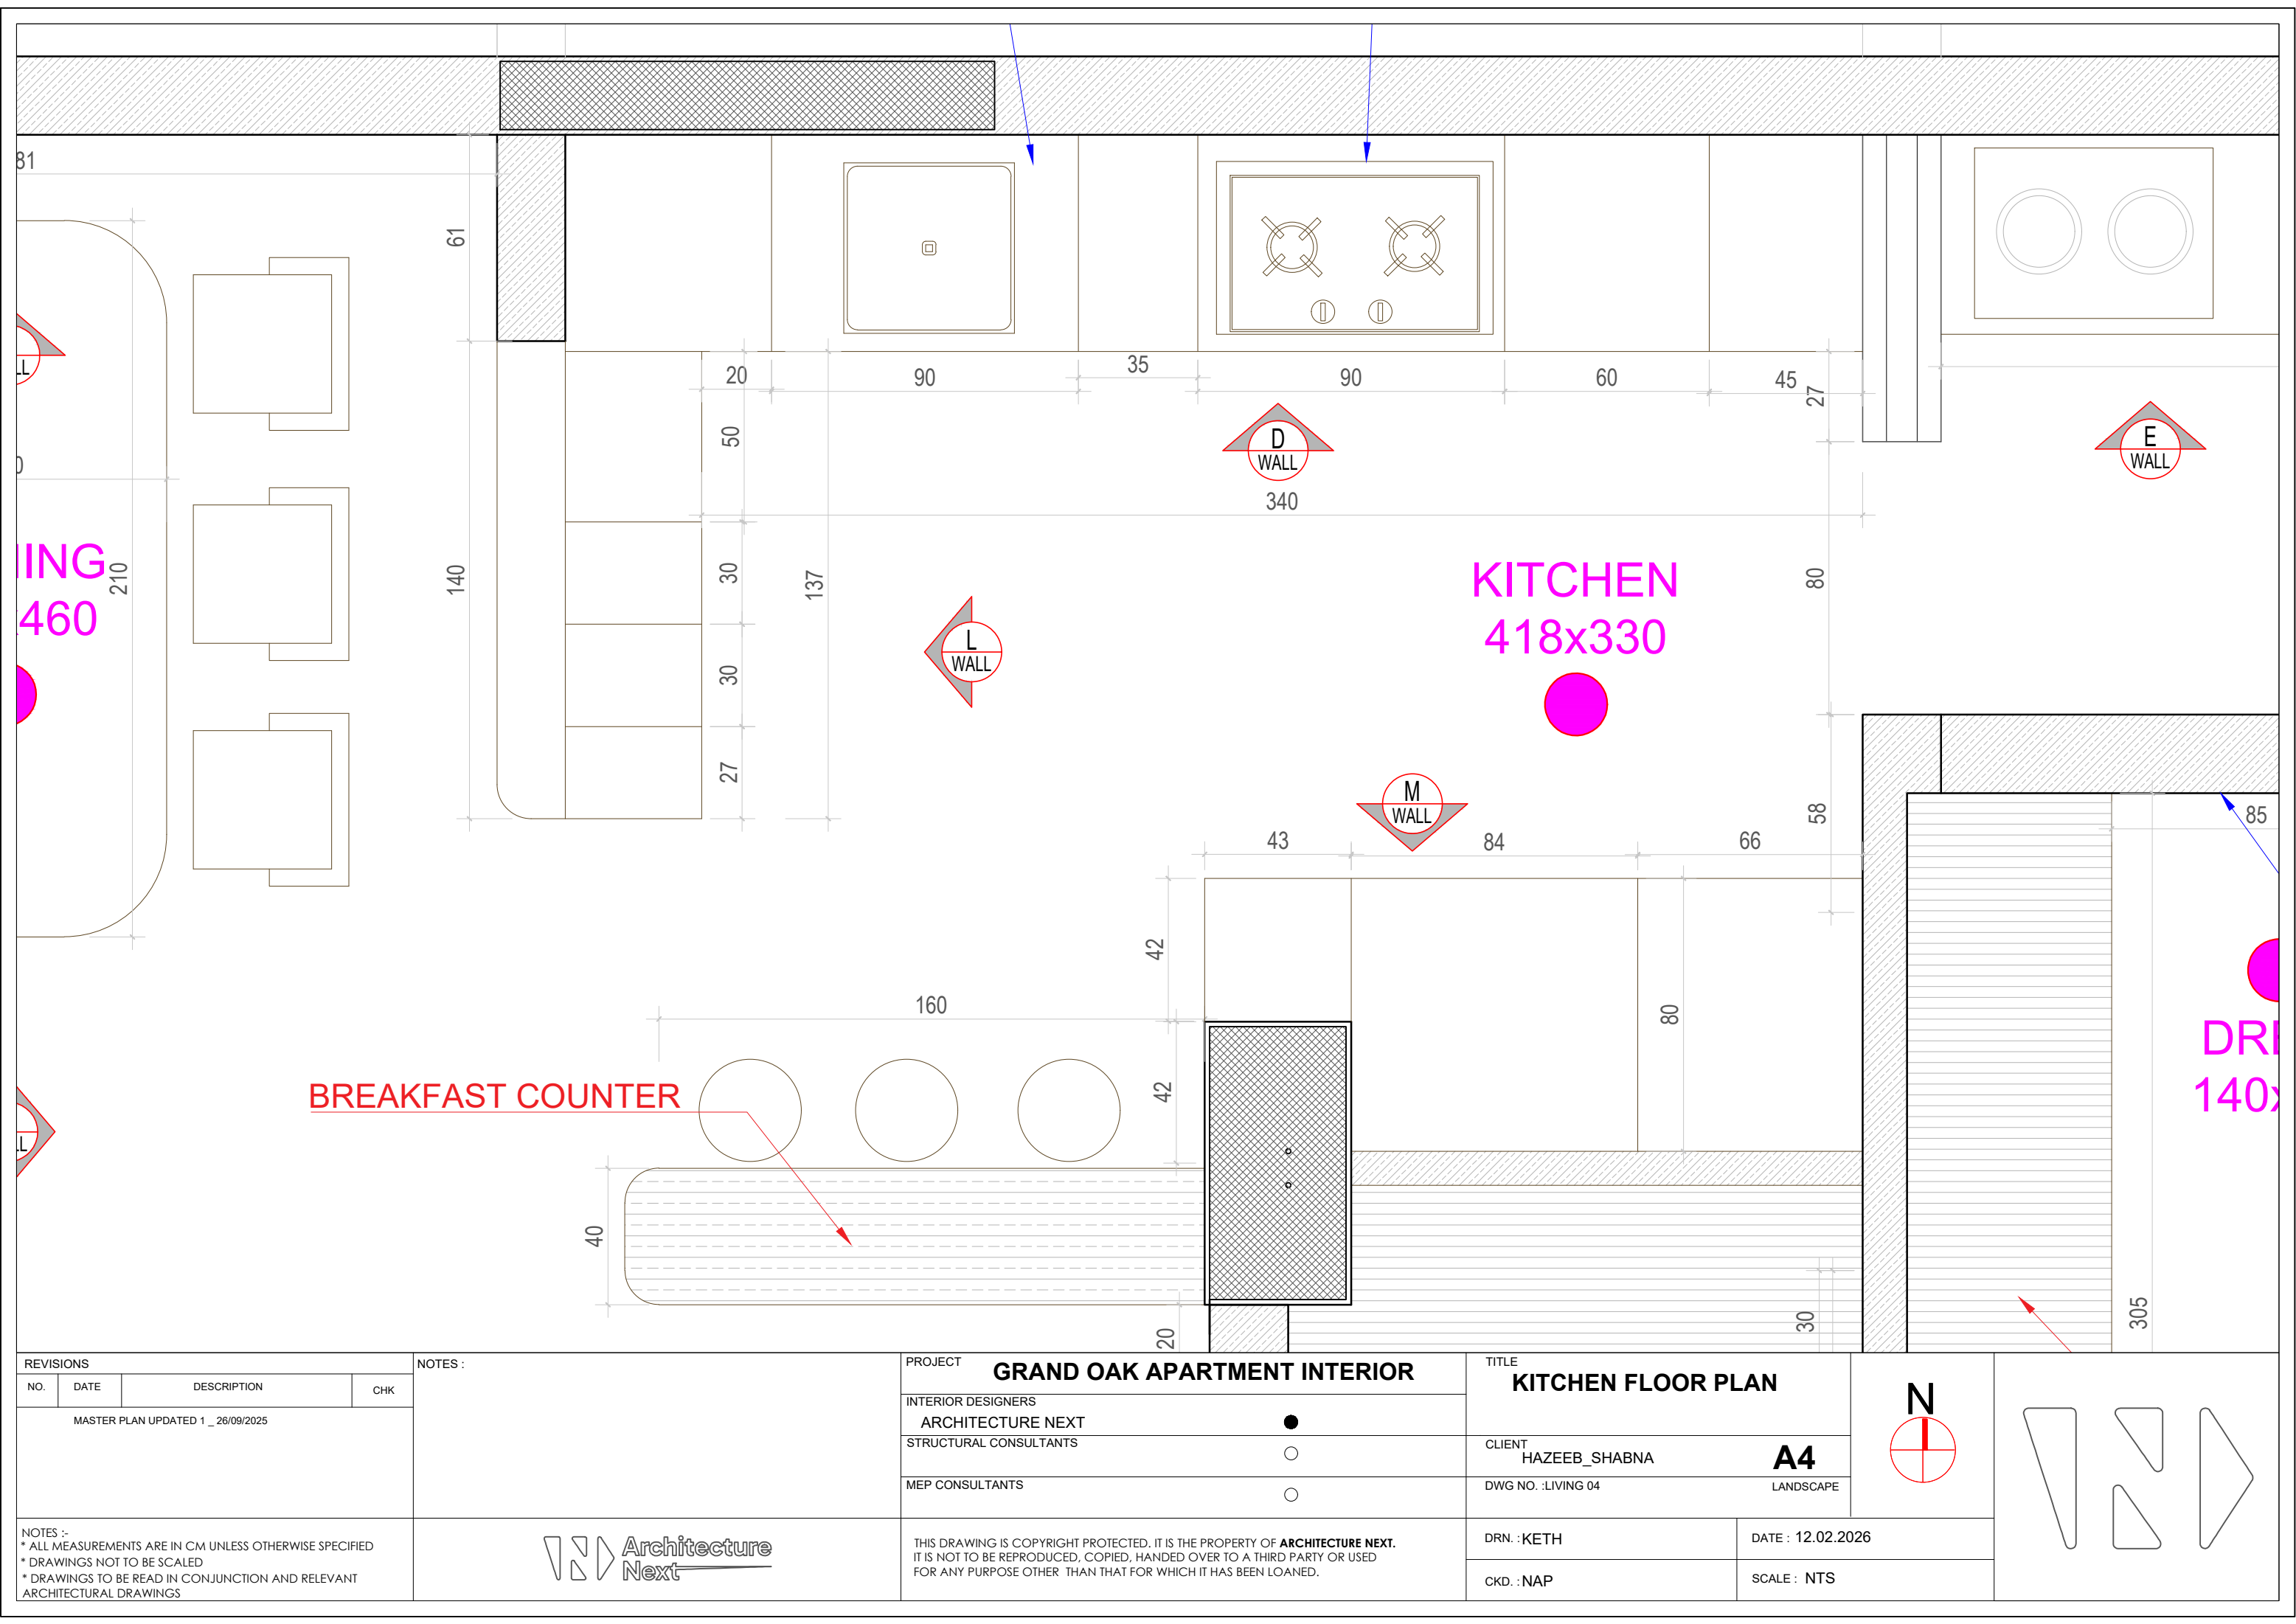

REVISIONS				NOTES :	PROJECT		TITLE		N		
NO.	DATE	DESCRIPTION	CHK		GRAND OAK APARTMENT INTERIOR		KITCHEN FLOOR PLAN				
MASTER PLAN UPDATED 1 _ 26/09/2025					INTERIOR DESIGNERS		CLIENT				
					ARCHITECTURE NEXT		HAZEEB_SHABNA				
					STRUCTURAL CONSULTANTS		DWG NO. :LIVING 04				
				MEP CONSULTANTS		LANDSCAPE					
NOTES :- * ALL MEASUREMENTS ARE IN CM UNLESS OTHERWISE SPECIFIED * DRAWINGS NOT TO BE SCALED * DRAWINGS TO BE READ IN CONJUNCTION AND RELEVANT ARCHITECTURAL DRAWINGS						THIS DRAWING IS COPYRIGHT PROTECTED. IT IS THE PROPERTY OF ARCHITECTURE NEXT. IT IS NOT TO BE REPRODUCED, COPIED, HANDED OVER TO A THIRD PARTY OR USED FOR ANY PURPOSE OTHER THAN THAT FOR WHICH IT HAS BEEN LOANED.		DRN. :KETH		DATE : 12.02.2026	
								CKD. :NAP		SCALE : NTS	

