


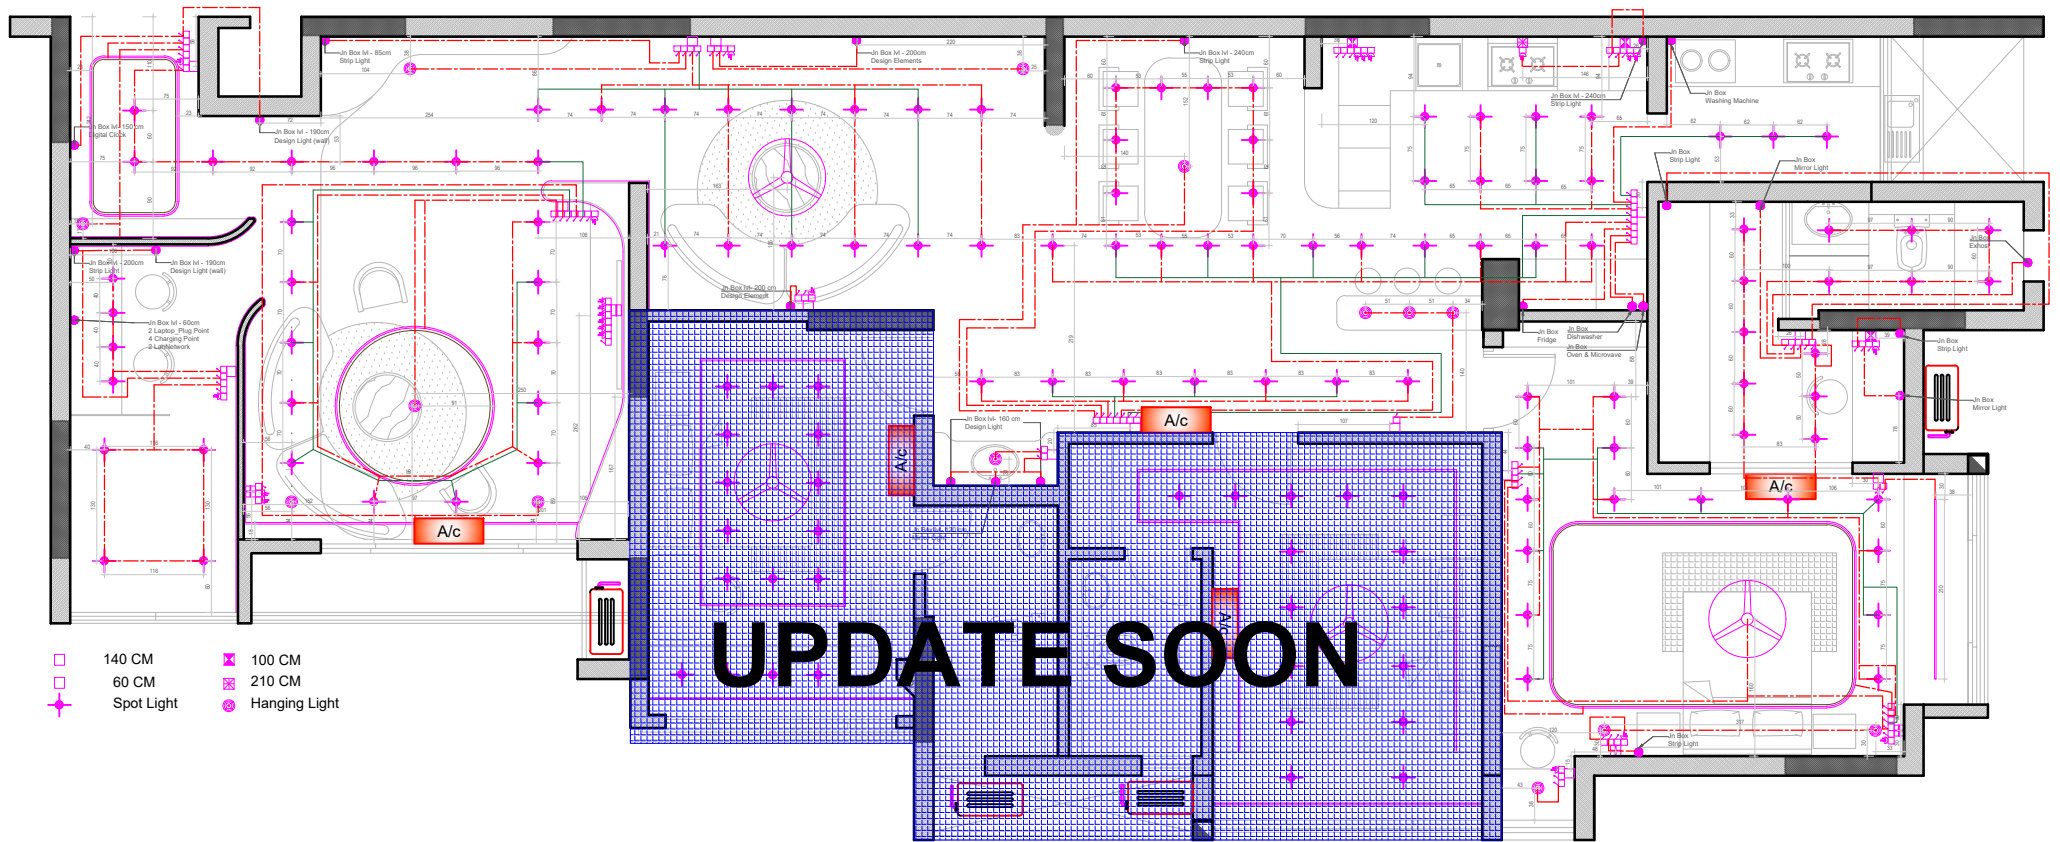

REVISIONS			
NO.	DATE	DESCRIPTION	CHK
DWG UPDATED 1_04/11/2025			
DWG UPDATED 2_04/11/2025			
NOTES :- * ALL MEASUREMENTS ARE IN CM UNLESS OTHERWISE SPECIFIED * DRAWINGS NOT TO BE SCALED * DRAWINGS TO BE READ IN CONJUNCTION AND RELEVANT ARCHITECTURAL DRAWINGS			

NOTES :			
PROJECT GRAND OAK APARTMENT INTERIOR			
INTERIOR DESIGNERS ARCHITECTURE NEXT			
STRUCTURAL CONSULTANTS			
MEP CONSULTANTS			
FIRST FLOOR HILITE BUSINESS PARK CALICUT 9995145694			

TITLE ELECTRICAL DRAWING			
CLIENT HAZEEB_SHABNA			
DWG NO. :003			
DRN. : KETH			
CKD. : NAP			

DATE : 28.09.2025	
SCALE : NTS	

N	
+91 9995 1456 94	