


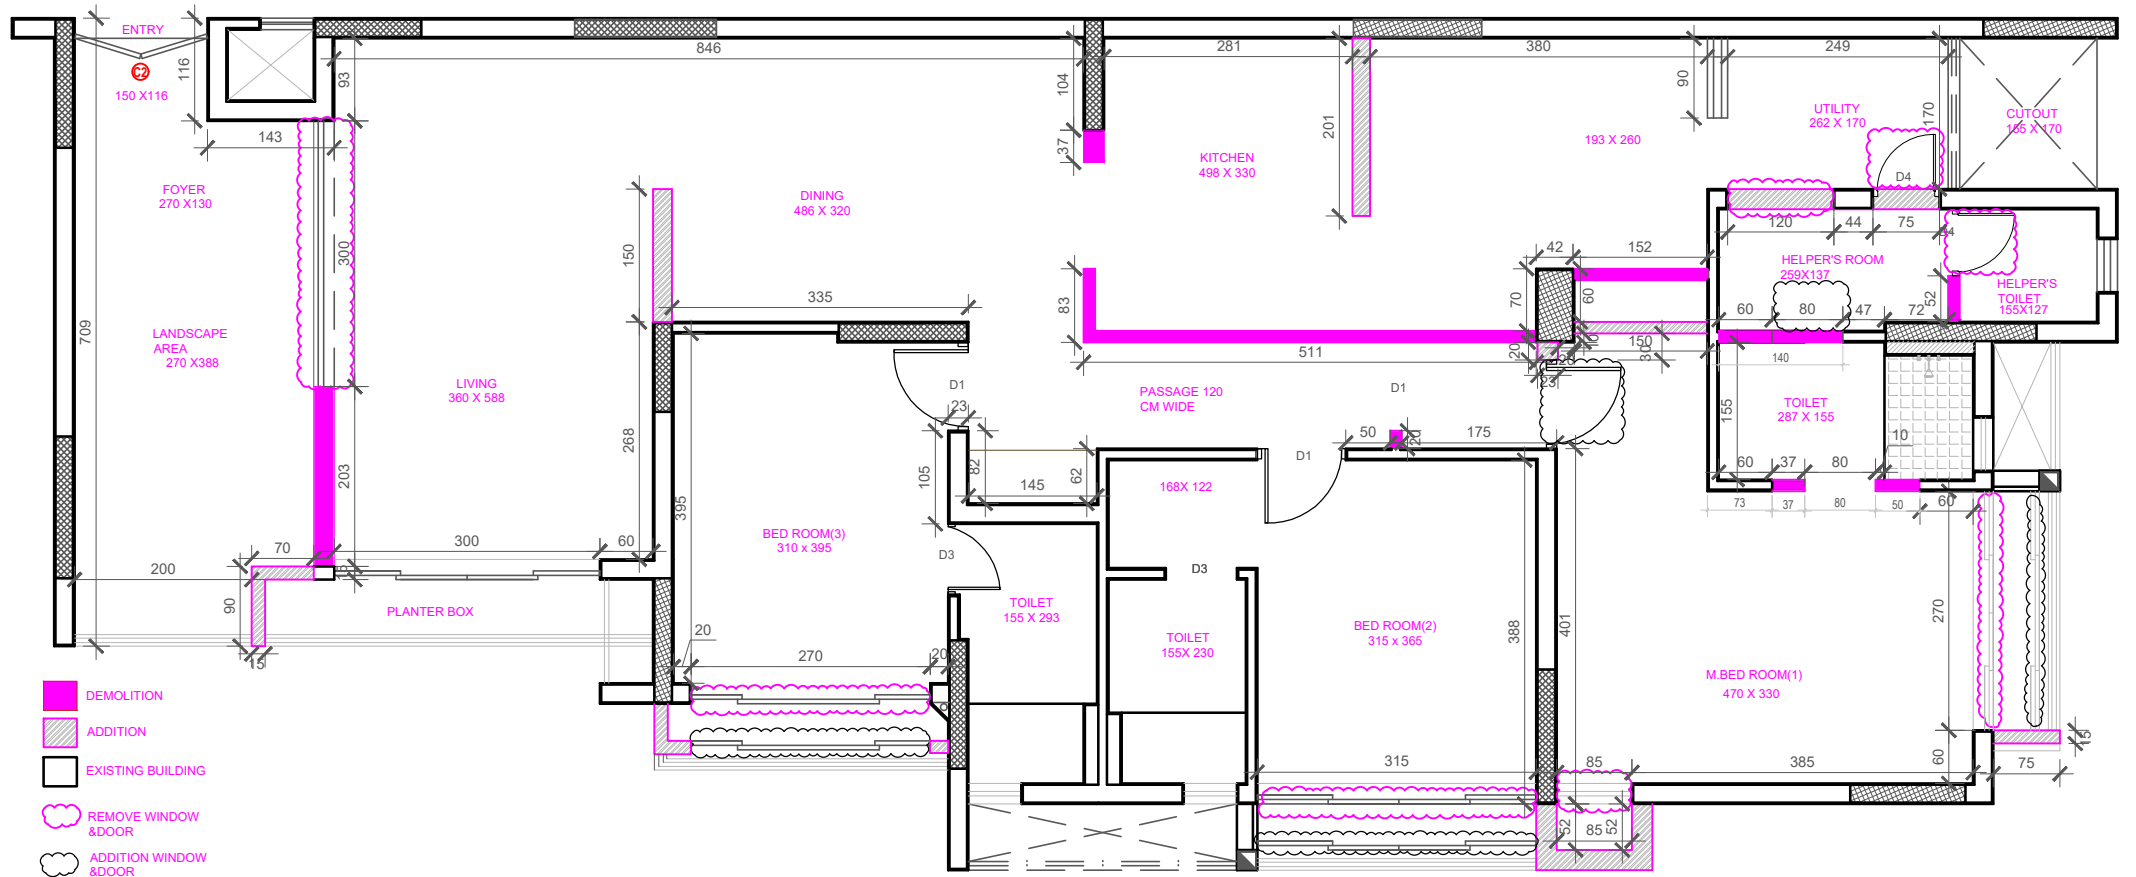

AREA DETAILS

FLOOR AREA : 190.26 SQM (2047.9 SQFT)  
CARPET AREA : 169.86 SQM (1828.3 SQFT)  
WALL : 23 CM

| REVISIONS   |      |             |     |
|---|------|-------------|-----|
| NO.   | DATE | DESCRIPTION | CHK |
|   |      |             |     |
| NOTES :-<br>* ALL MEASUREMENTS ARE IN CM UNLESS OTHERWISE SPECIFIED<br>* DRAWINGS NOT TO BE SCALED<br>* DRAWINGS TO BE READ IN CONJUNCTION AND RELEVANT ARCHITECTURAL DRAWINGS |      |             |     |


| NOTES : |  |
|---------|--|
|         |  |
|         |  |
|         |  |
|         |  |

| PROJECT                      |   |
|------------------------------|---|
| GRAND OAK APARTMENT INTERIOR |   |
| INTERIOR DESIGNERS           | ● |
| ARCHITECTURE NEXT            |   |
| STRUCTURAL CONSULTANTS       | ○ |
| MEP CONSULTANTS              | ○ |

| TITLE                 |                   |
|-----------------------|-------------------|
| DEMOLITION & ADDITION |                   |
| CLIENT                | HAZEEB_SHABNA     |
| DWG NO. :002          | A4 LANDSCAPE      |
| DRN. : KETH           | DATE : 28.09.2025 |
| CKD. : NAP            | SCALE : NTS       |



+91 9995 1456 94

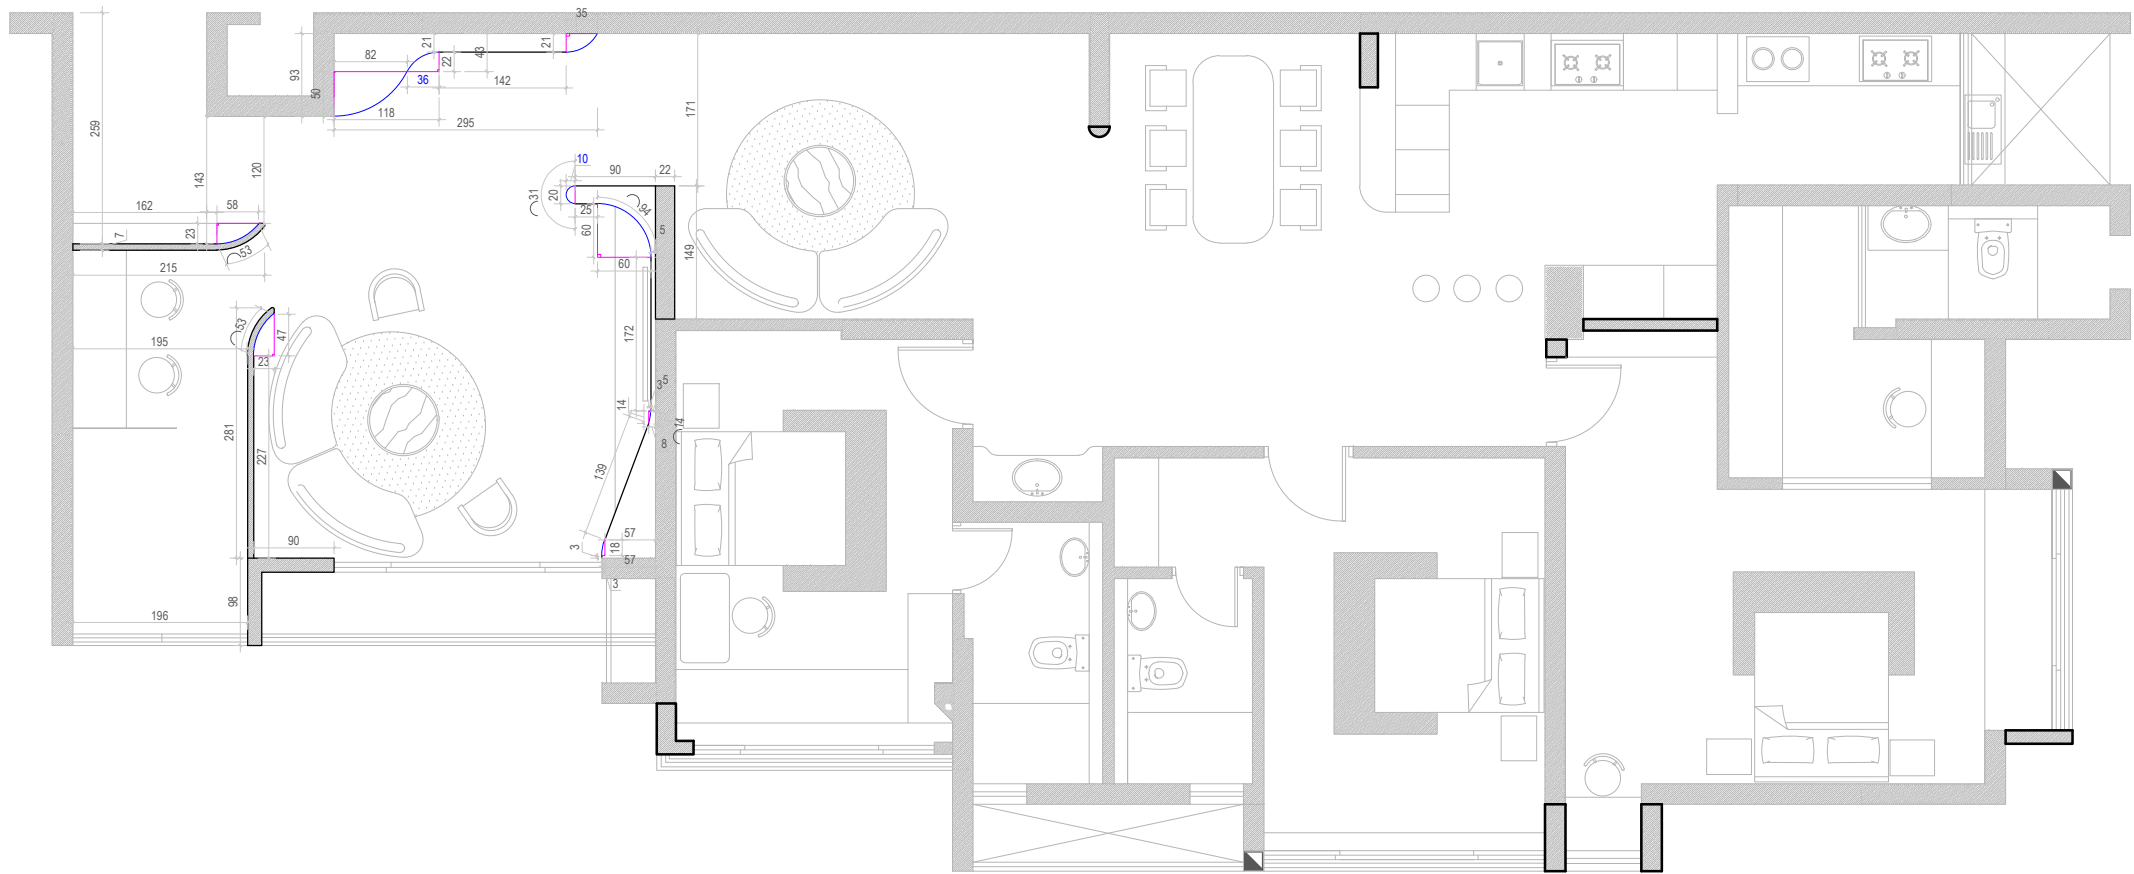

| REVISIONS   |      |             |     |
|---|------|-------------|-----|
| NO.   | DATE | DESCRIPTION | CHK |
|   |      |             |     |
| NOTES :-<br>* ALL MEASUREMENTS ARE IN CM UNLESS OTHERWISE SPECIFIED<br>* DRAWINGS NOT TO BE SCALED<br>* DRAWINGS TO BE READ IN CONJUNCTION AND RELEVANT ARCHITECTURAL DRAWINGS |      |             |     |

NOTES :

Architecture

Next

FIRST FLOOR | HILITE BUSINESS PARK | CALICUT | 9995145694

| PROJECT                      |   |
|------------------------------|---|
| GRAND OAK APARTMENT INTERIOR |   |
| INTERIOR DESIGNERS           | ● |
| ARCHITECTURE NEXT            | ○ |
| STRUCTURAL CONSULTANTS       | ○ |
| MEP CONSULTANTS              | ○ |

| TITLE         |                   |
|---------------|-------------------|
| ADDITION PLAN |                   |
| CLIENT        | HAZEEB_SHABNA     |
| DWG NO. :     | A4                |
| DRN. : KETH   | DATE : 07.09.2025 |
| CKD. : NAP    | SCALE : NTS       |

N

+91 9995 1456 94