


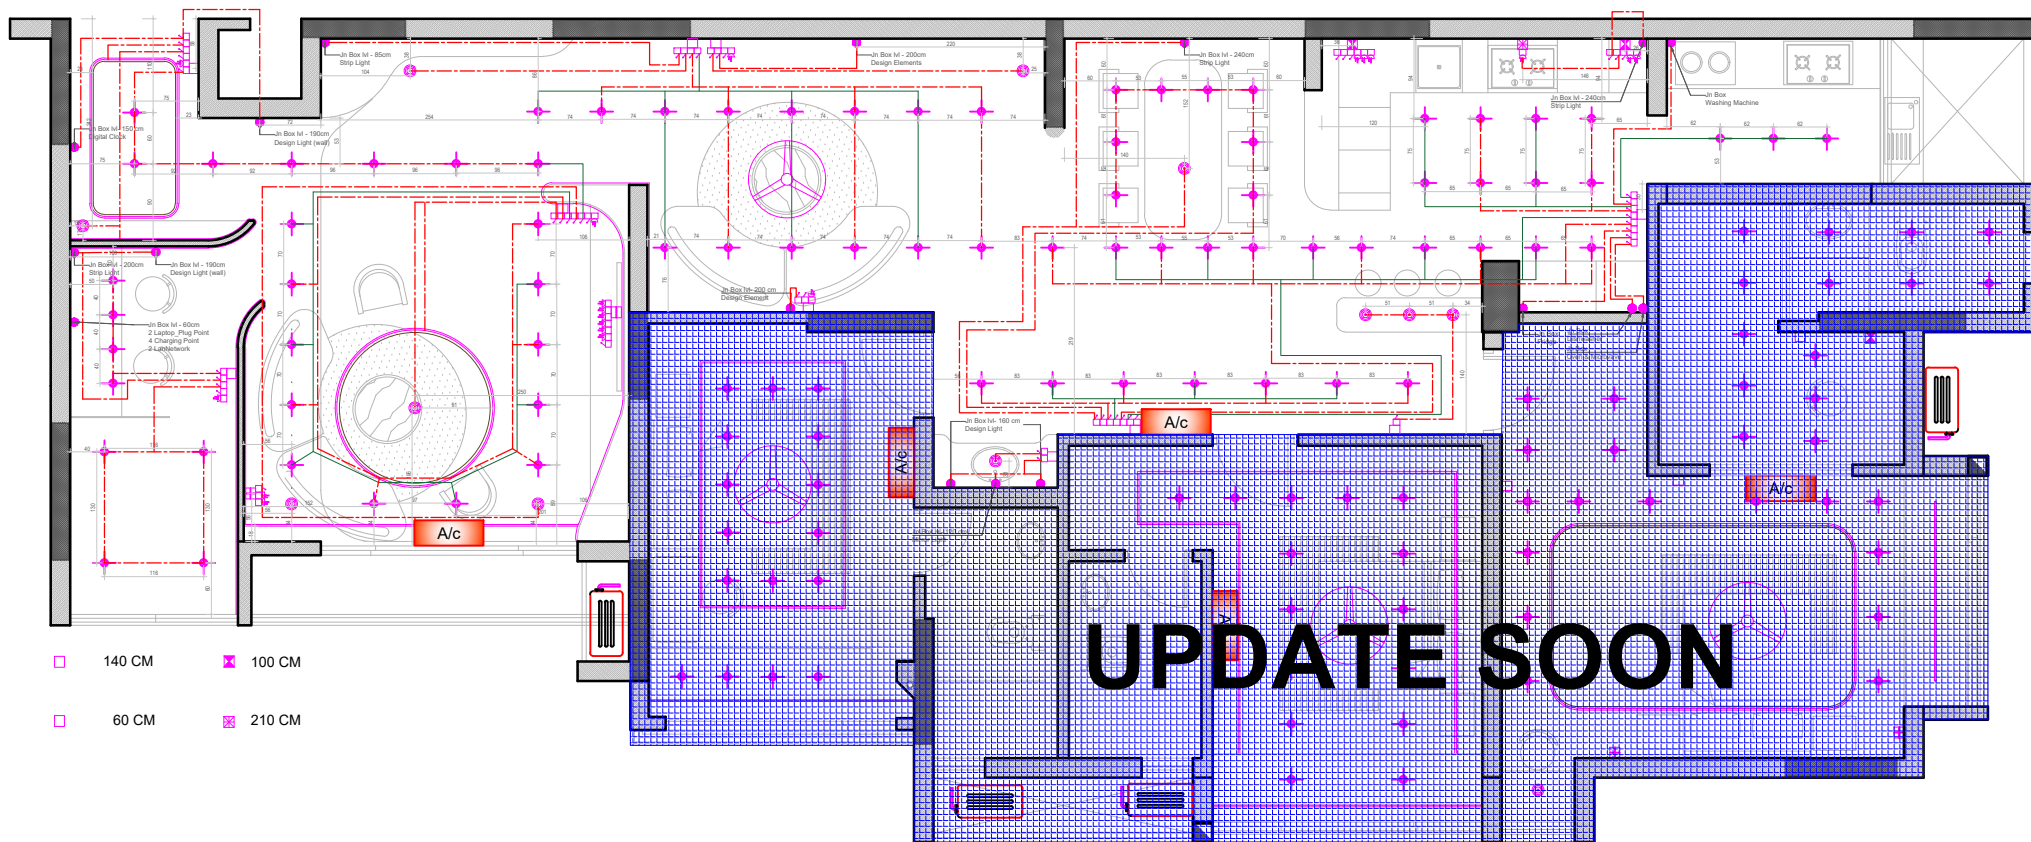

REVISIONS			
NO.	DATE	DESCRIPTION	CHK

DWG UPDATED 1 _ 04/11/2025

NOTES :-
* ALL MEASUREMENTS ARE IN CM UNLESS OTHERWISE SPECIFIED
* DRAWINGS NOT TO BE SCALED
* DRAWINGS TO BE READ IN CONJUNCTION AND RELEVANT ARCHITECTURAL DRAWINGS

NOTES :

Architecture
Next
FIRST FLOOR | HILITE BUSINESS PARK | CALICUT | 9995145694

PROJECT **GRAND OAK APARTMENT INTERIOR**

INTERIOR DESIGNERS
ARCHITECTURE NEXT
STRUCTURAL CONSULTANTS
MEP CONSULTANTS

TITLE
ELECTRICAL DRAWING

CLIENT
HAZEEB_SHABNA
DWG NO. :003

DRN. : KETH
CKD. : NAP

N

A4
LANDSCAPE

DATE : 28.09.2025
SCALE : NTS


+91 9995 1456 94

THIS DRAWING IS COPYRIGHT PROTECTED, IT IS THE PROPERTY OF **ARCHITECTURE NEXT**. IT IS NOT TO BE REPRODUCED, COPIED, HANDED OVER TO A THIRD PARTY OR USED FOR ANY PURPOSE OTHER THAN THAT FOR WHICH IT HAS BEEN LOANED.