


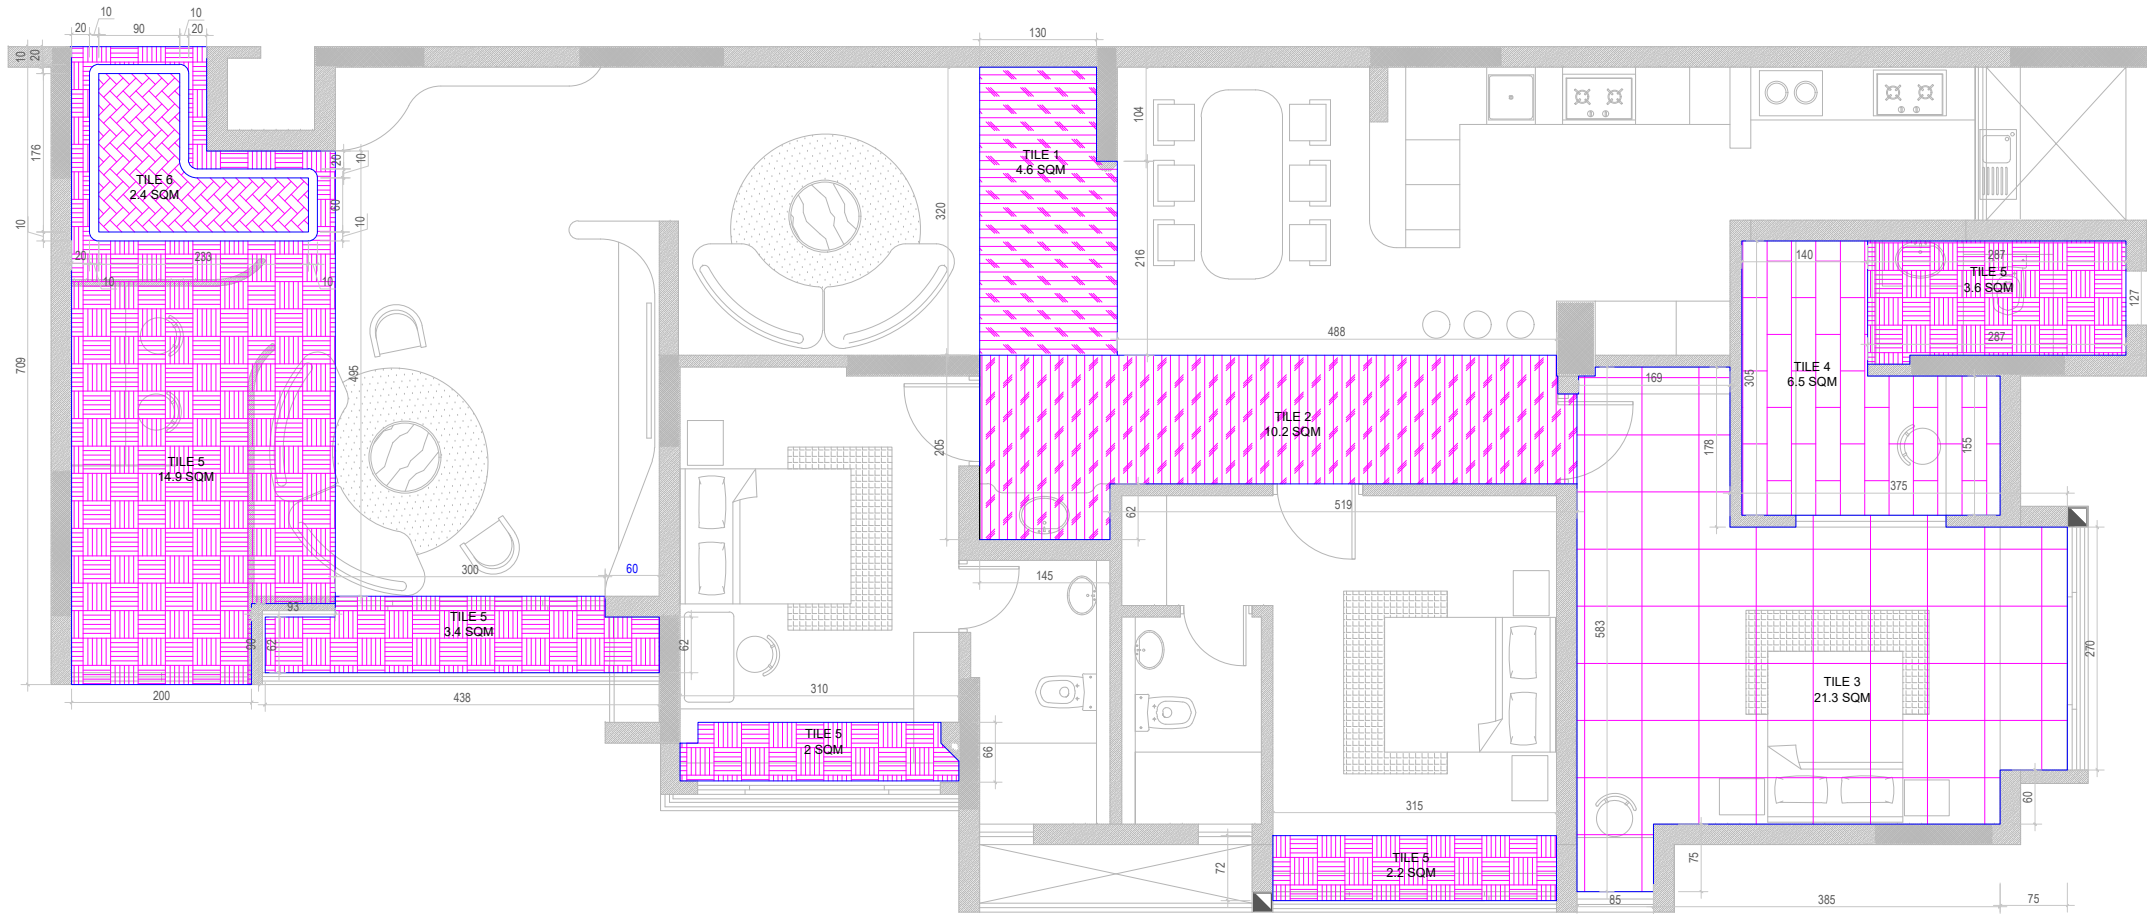

REVISIONS			
NO.	DATE	DESCRIPTION	CHK

NOTES :

NOTES :-
* ALL MEASUREMENTS ARE IN CM UNLESS OTHERWISE SPECIFIED
* DRAWINGS NOT TO BE SCALED
* DRAWINGS TO BE READ IN CONJUNCTION AND RELEVANT ARCHITECTURAL DRAWINGS


Architecture
Next
FIRST FLOOR | HILITE BUSINESS PARK | CALICUT | 9995145694

PROJECT	
GRAND OAK APARTMENT INTERIOR	
INTERIOR DESIGNERS	●
ARCHITECTURE NEXT	
STRUCTURAL CONSULTANTS	○
MEP CONSULTANTS	○

THIS DRAWING IS COPYRIGHT PROTECTED, IT IS THE PROPERTY OF **ARCHITECTURE NEXT**. IT IS NOT TO BE REPRODUCED, COPIED, HANDED OVER TO A THIRD PARTY OR USED FOR ANY PURPOSE OTHER THAN THAT FOR WHICH IT HAS BEEN LOANED.

TITLE	
TILE LAYOUT	
CLIENT	HAZEEB_SHABNA
DWG NO. : 005	A4 LANDSCAPE

DRN. : KETH	DATE : 08.11.2025
CKD. : NAP	SCALE : NTS

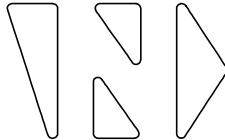

+91 9995 1456 94