


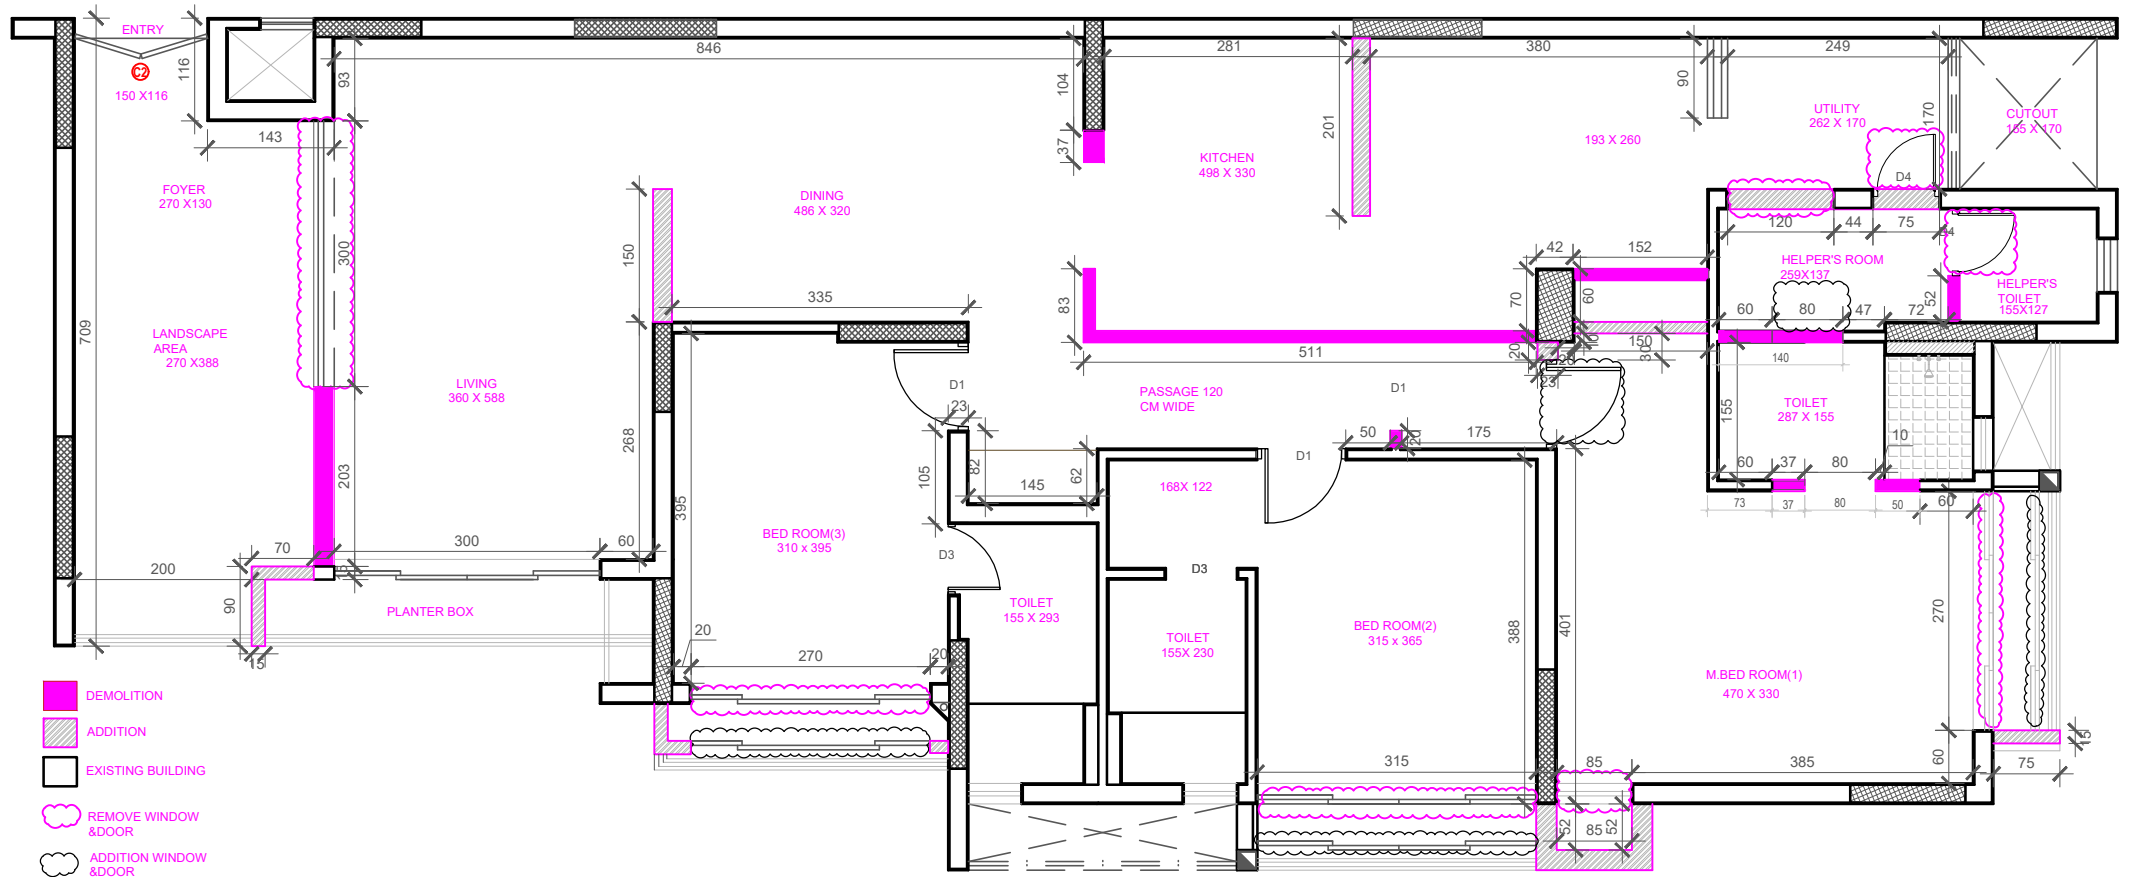

AREA DETAILS

FLOOR AREA : 190.26 SQM (2047.9 SQFT)
CARPET AREA : 169.86 SQM (1828.3 SQFT)
WALL : 23 CM

REVISIONS			
NO.	DATE	DESCRIPTION	CHK
NOTES :- * ALL MEASUREMENTS ARE IN CM UNLESS OTHERWISE SPECIFIED * DRAWINGS NOT TO BE SCALED * DRAWINGS TO BE READ IN CONJUNCTION AND RELEVANT ARCHITECTURAL DRAWINGS			

NOTES :

Architecture
Next

FIRST FLOOR | HILITE BUSINESS PARK | CALICUT | 9995145694

PROJECT		TITLE	
GRAND OAK APARTMENT INTERIOR		DEMOLITION & ADDITION	
INTERIOR DESIGNERS ARCHITECTURE NEXT		CLIENT HAZEEB_SHABNA	
STRUCTURAL CONSULTANTS		DWG NO. :002	
MEP CONSULTANTS		LANDSCAPE	
THIS DRAWING IS COPYRIGHT PROTECTED, IT IS THE PROPERTY OF ARCHITECTURE NEXT. IT IS NOT TO BE REPRODUCED, COPIED, HANDED OVER TO A THIRD PARTY OR USED FOR ANY PURPOSE OTHER THAN THAT FOR WHICH IT HAS BEEN LOANED.		DRN. : KETH	
		DATE : 28.09.2025	
		CKD. : NAP	
		SCALE : NTS	

N

HAZEEB_SHABNA

A4

DRN. : KETH

DATE : 28.09.2025

CKD. : NAP

SCALE : NTS

HAZEEB_SHABNA

A4


DRN. : KETH

DATE : 28.09.2025

CKD. : NAP

SCALE : NTS

+91 9995 1456 94

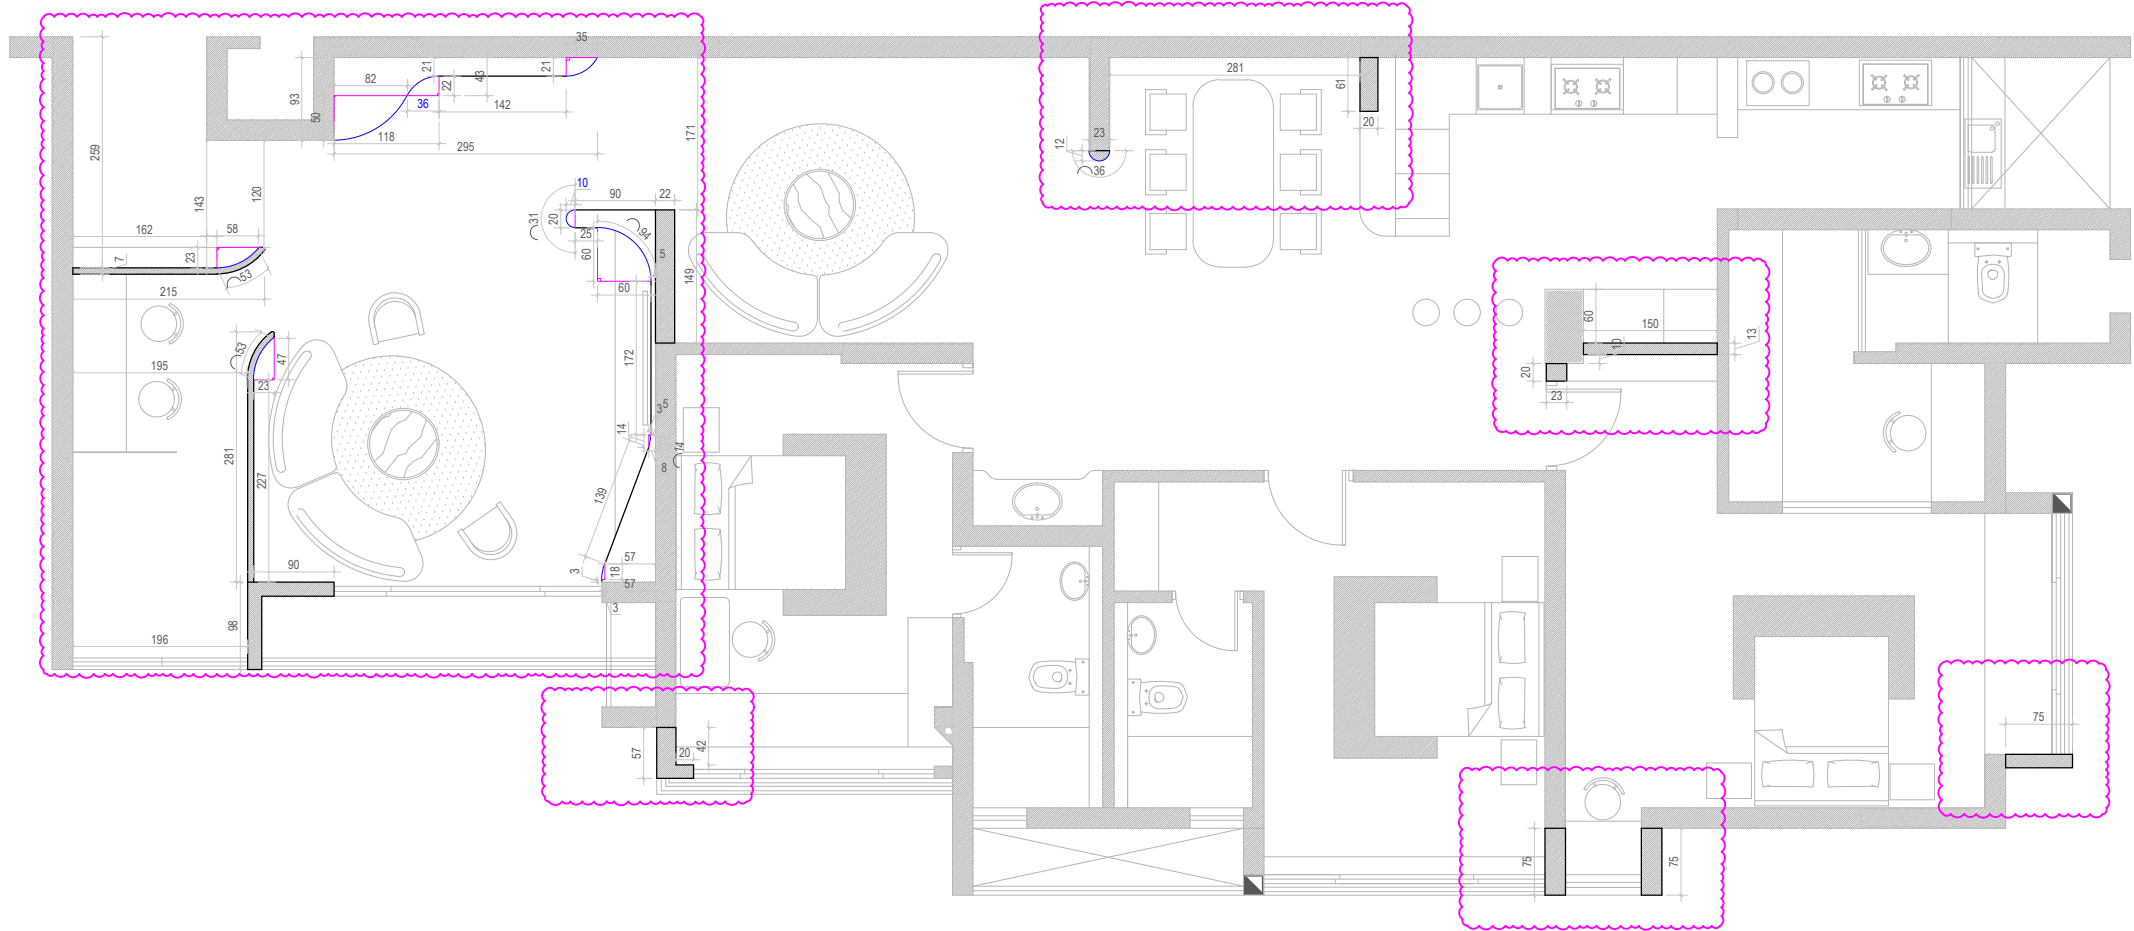

REVISIONS			
NO.	DATE	DESCRIPTION	CHK
NOTES :- * ALL MEASUREMENTS ARE IN CM UNLESS OTHERWISE SPECIFIED * DRAWINGS NOT TO BE SCALED * DRAWINGS TO BE READ IN CONJUNCTION AND RELEVANT ARCHITECTURAL DRAWINGS			

NOTES :

Architecture Next
FIRST FLOOR | HILITE BUSINESS PARK | CALICUT | 9995145694

PROJECT		TITLE	
GRAND OAK APARTMENT INTERIOR		ADDITION PLAN	
INTERIOR DESIGNERS ARCHITECTURE NEXT		CLIENT HAZEEB_SHABNA	
STRUCTURAL CONSULTANTS		A4	
MEP CONSULTANTS		LANDSCAPE	
THIS DRAWING IS COPYRIGHT PROTECTED, IT IS THE PROPERTY OF ARCHITECTURE NEXT. IT IS NOT TO BE REPRODUCED, COPIED, HANDED OVER TO A THIRD PARTY OR USED FOR ANY PURPOSE OTHER THAN THAT FOR WHICH IT HAS BEEN LOANED.		DRN. : KETH	DATE : 07.09.2025
		CKD. : NAP	SCALE : NTS

North Arrow (N) pointing up.

Scale: NTS

Architectural logo consisting of three stylized, overlapping shapes.

+91 9995 1456 94