


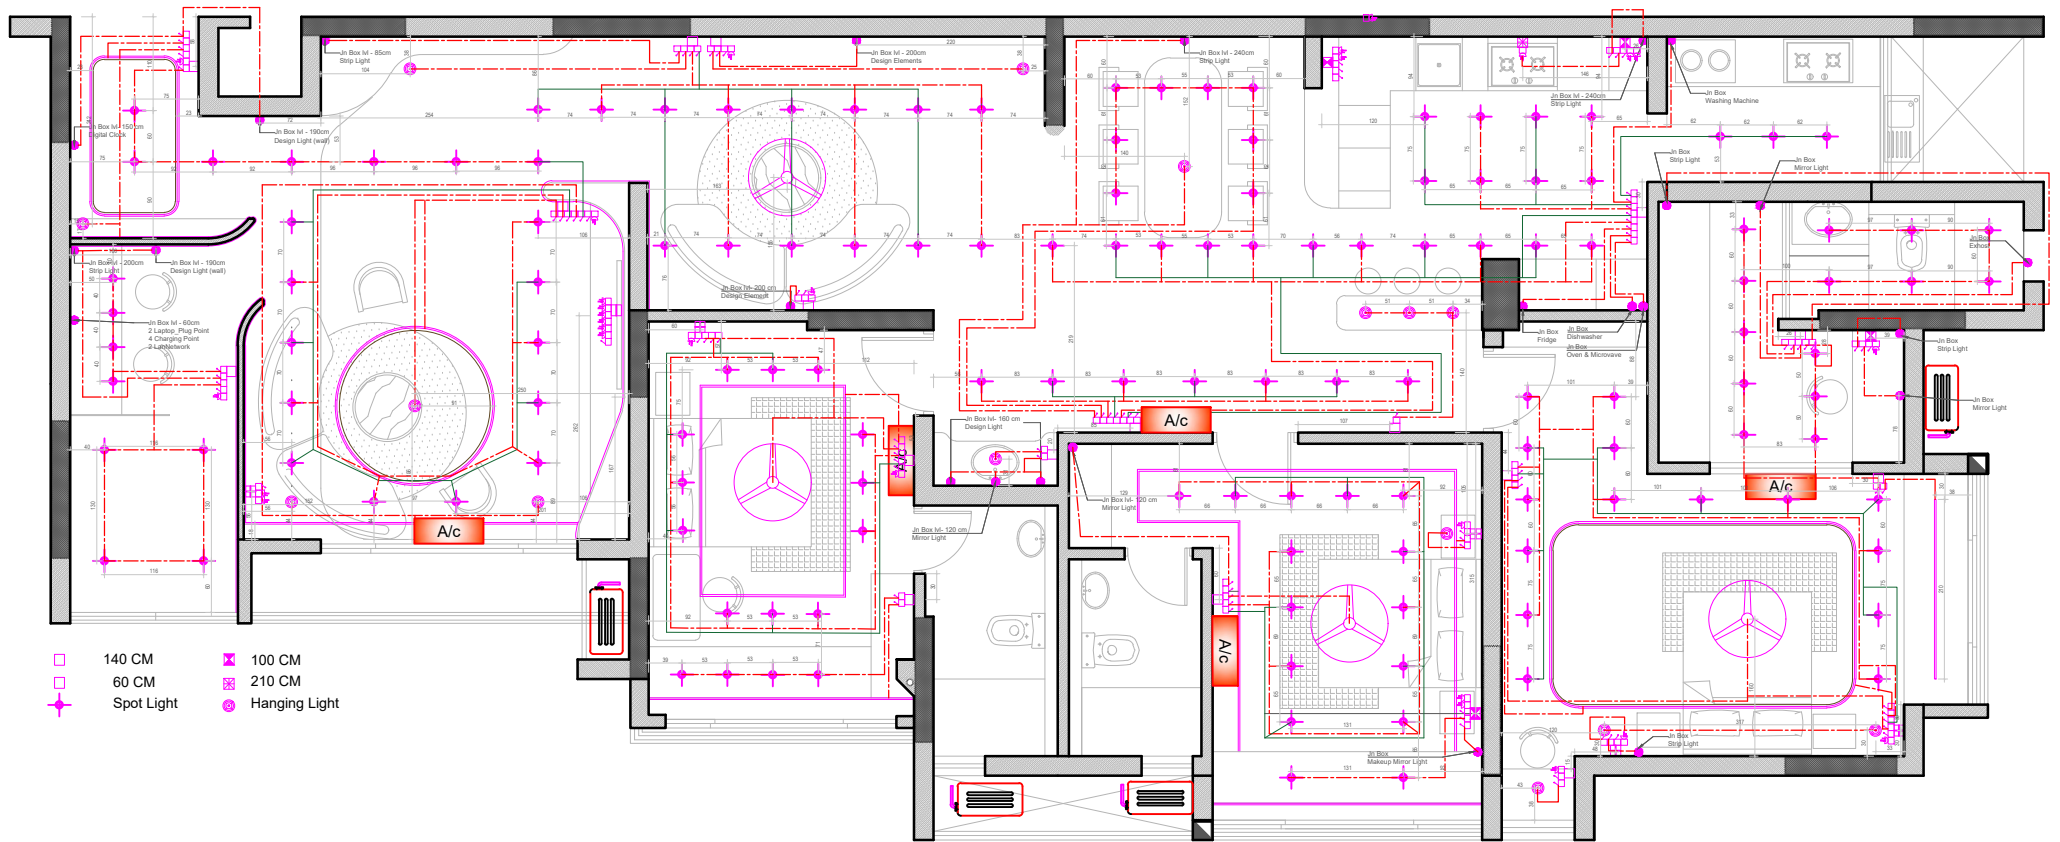

REVISIONS			
NO.	DATE	DESCRIPTION	CHK
1	04/11/2025	DWG UPDATED 1	
2	04/11/2025	DWG UPDATED 2	
3	07/11/2025	DWG UPDATED 3	

NOTES :-
* ALL MEASUREMENTS ARE IN CM UNLESS OTHERWISE SPECIFIED
* DRAWINGS NOT TO BE SCALED
* DRAWINGS TO BE READ IN CONJUNCTION AND RELEVANT ARCHITECTURAL DRAWINGS


NOTES :			


Architecture
Next
FIRST FLOOR | HILITE BUSINESS PARK | CALICUT | 9995145694

PROJECT	
GRAND OAK APARTMENT INTERIOR	
INTERIOR DESIGNERS	●
ARCHITECTURE NEXT	○
STRUCTURAL CONSULTANTS	○
MEP CONSULTANTS	○

THIS DRAWING IS COPYRIGHT PROTECTED, IT IS THE PROPERTY OF ARCHITECTURE NEXT. IT IS NOT TO BE REPRODUCED, COPIED, HANDED OVER TO A THIRD PARTY OR USED FOR ANY PURPOSE OTHER THAN THAT FOR WHICH IT HAS BEEN LOANED.

TITLE	
ELECTRICAL DRAWING	
CLIENT	HAZEEB_SHABNA
DWG NO. :003	A4 LANDSCAPE
DRN. : KETH	DATE : 28.09.2025
CKD. : NAP	SCALE : NTS

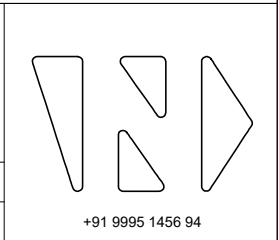

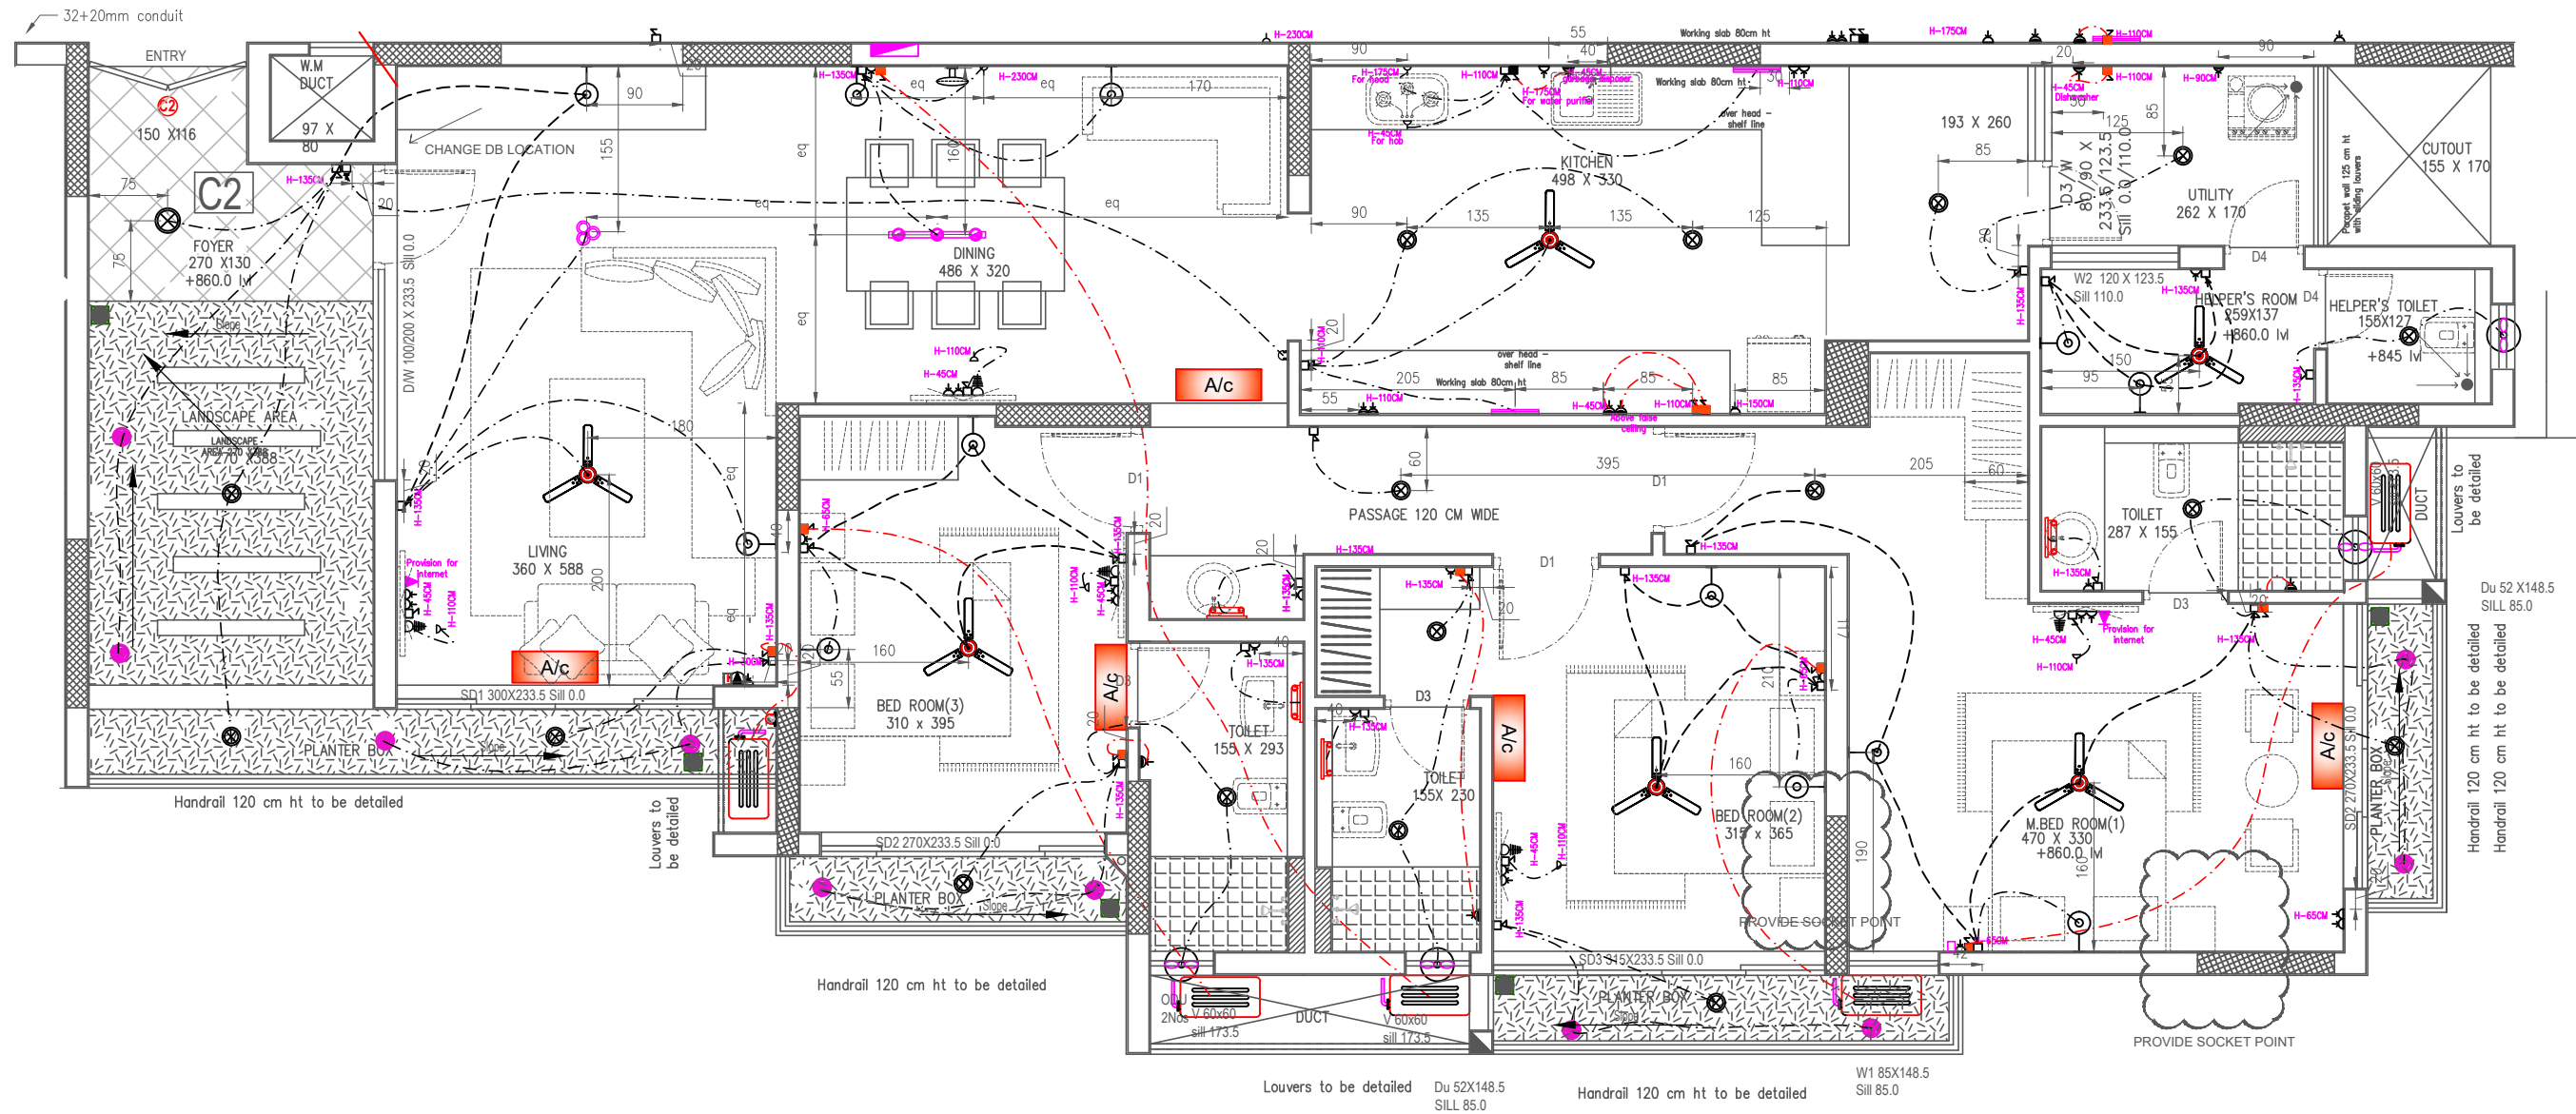

Symbol	Description
	Distribution board
	Ceiling fan
	Exhaust fan
	Bracket light
	Kitchen cabinet light
	Ceiling light
	6A socket
	6A socket with switch
	16A socket with switch
	16A socket
	6A switch board
	16A switch
	20A switch
	A/C indoor unit
	A/C outdoor unit
	Data outlet
	Telephone outlet
	Mirror light
	Bollard
	Hanging light
	Chandelier
	Bell push
	Door bell
	Wall fan
	Antenna point
	Points on Inverter/UPS
	CCTV Camera
	Intercom
	USB socket
	Motion Sensor

REV.	DESCRIPTION	DATE
0	FOR APPROVAL	29/08/16

PURPOSE OF ISSUING:
FOR APPROVAL

PROJECT:
GRAND OAK,CALICUT

CLIENT:
MALABAR DEVELOPERS.

ARCHITECT:
STAPATI
calicut
architecture - planning - interiors
5 / 2759 C, Kalipolka, Mini by pass rd., Calicut, Kerala
673 004, India. t : + 91 495 2771102, 2771103
f : + 91 495 2771101 e : calicut@stapati.com

TITLE:
ELECTRICAL LAYOUT FOR
TYPICAL FLOORS

DRAWN BY:	CHECKED BY:	APPROVED BY:
AP	BUJU	SABU
JOB No.:	DWG No.:	DATE
EC 279	ECC/STC279EL-04	29/08/2016
SCALE:	REV. No.:	SIZE
NTS	0	A2

ELECTRICAL CONSULTANT:
eccentre
building service consultants
A-20, Ratnam Square
West Nadakkavu,
Calicut - 673 011
Ph: +91 495 4044798,
+91 495 2367707
Email: eccentre@gmail.com

THIS DRAWING IS THE SOLE PROPERTY OF EC CENTRE.
IT'S USE FOR ANY PURPOSE OTHER THAN THAT MENTIONED
IS TO BE DONE ONLY AFTER PRIOR APPROVAL.