


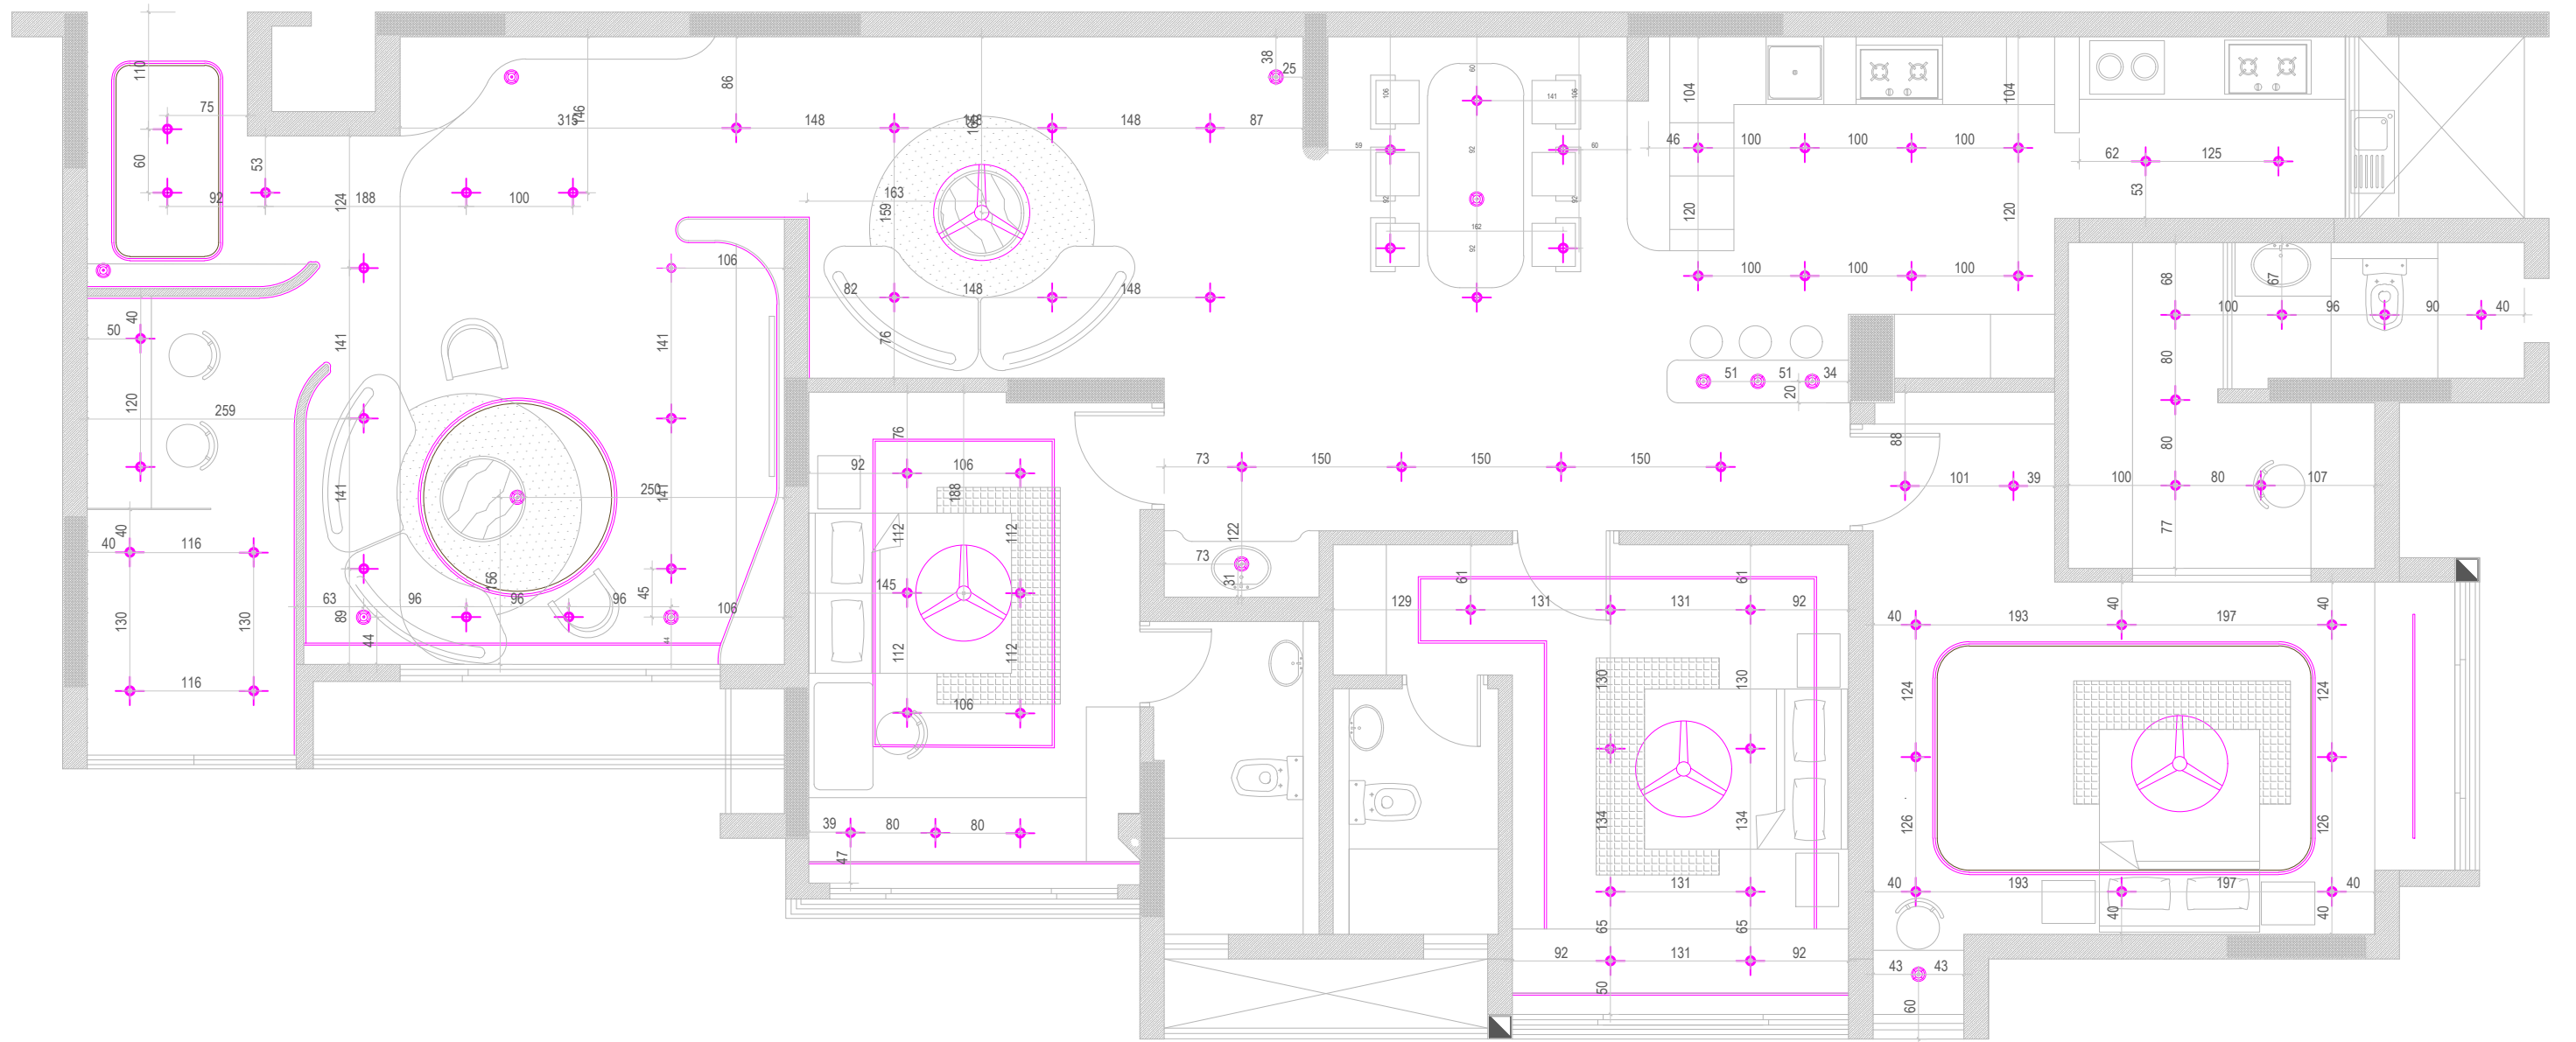


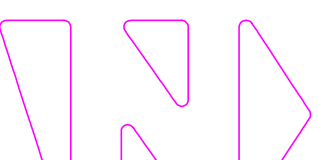


REVISIONS				NOTES :	PROJECT		TITLE		N 	 +91 9995 1456 94
NO.	DATE	DESCRIPTION	CHK		GRAND OAK APARTMENT INTERIOR		CEILING LIGHTS DETAILS			
					INTERIOR DESIGNERS ARCHITECTURE NEXT		CLIENT HAZEEB_SHABNA			
					STRUCTURAL CONSULTANTS		A4			
					MEP CONSULTANTS		DWG NO. :003			
NOTES :- * ALL MEASUREMENTS ARE IN CM UNLESS OTHERWISE SPECIFIED * DRAWINGS NOT TO BE SCALED * DRAWINGS TO BE READ IN CONJUNCTION AND RELEVANT ARCHITECTURAL DRAWINGS				 FIRST FLOOR HILITE BUSINESS PARK CALICUT 9995145694		THIS DRAWING IS COPYRIGHT PROTECTED. IT IS THE PROPERTY OF ARCHITECTURE NEXT . IT IS NOT TO BE REPRODUCED, COPIED, HANDED OVER TO A THIRD PARTY OR USED FOR ANY PURPOSE OTHER THAN THAT FOR WHICH IT HAS BEEN LOANED.		DRN. :KETH		DATE : 01.12.2025
						CKD. :NAP		SCALE : NTS		

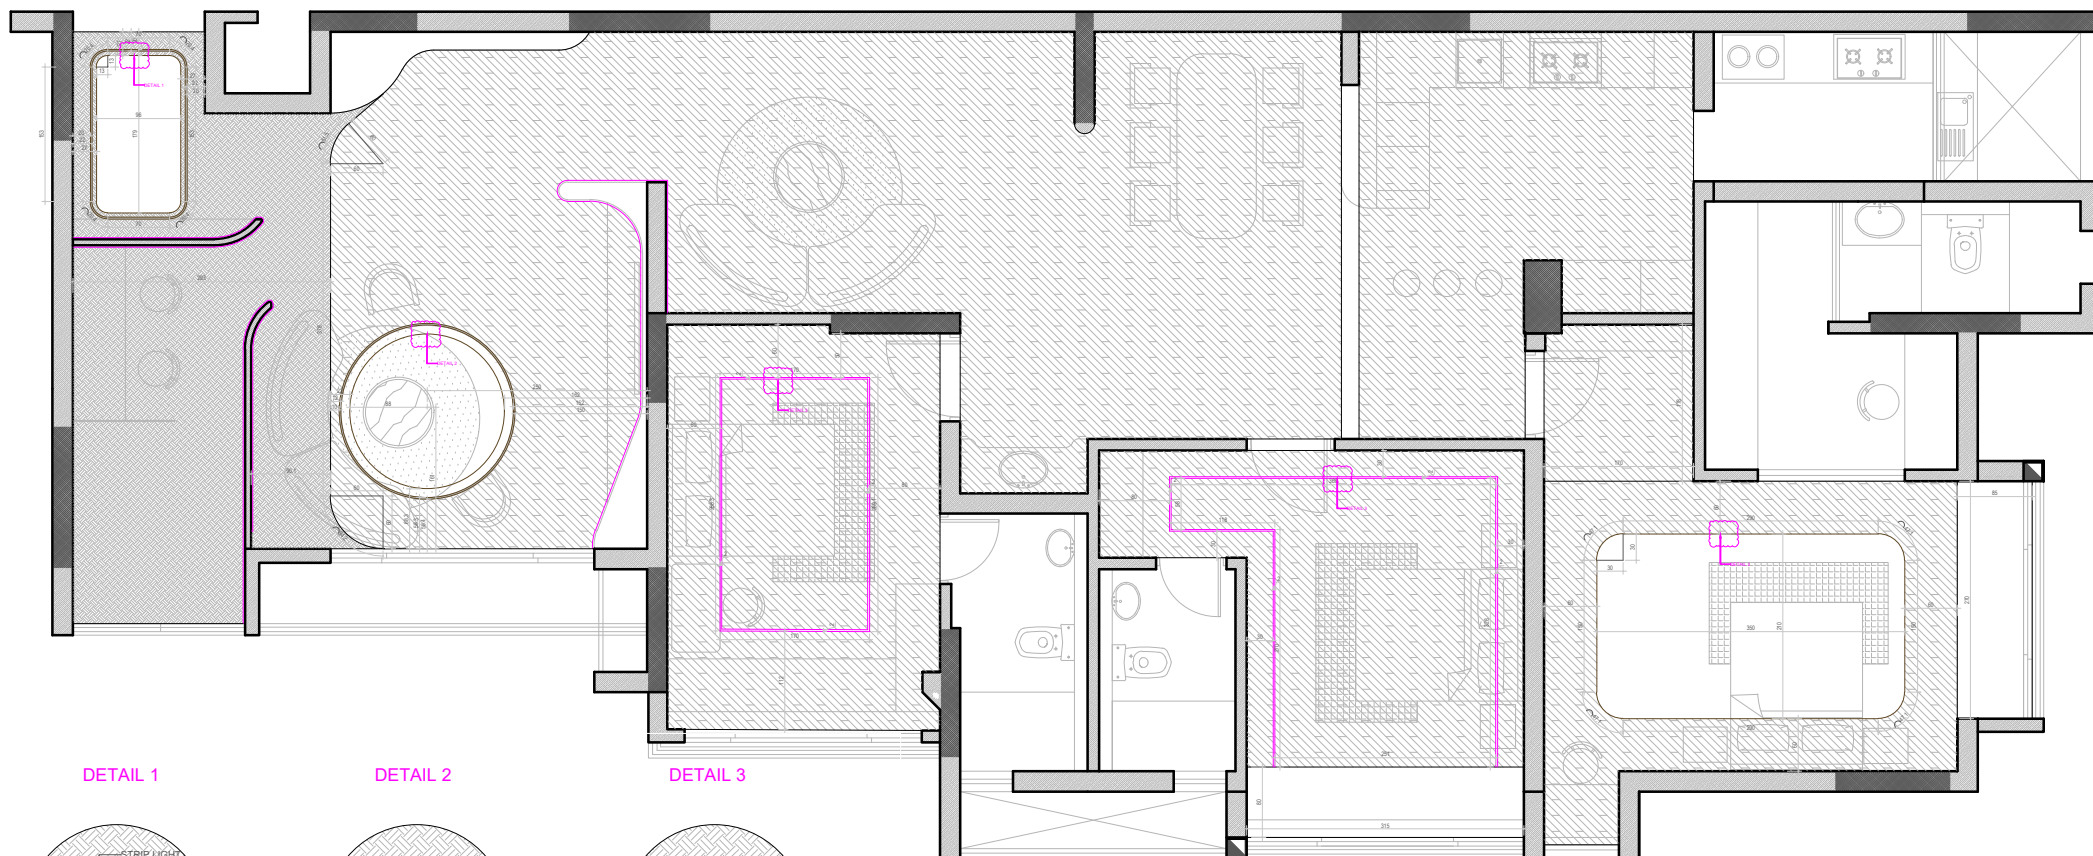


DETAIL 1

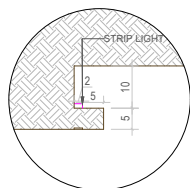

DETAIL 2

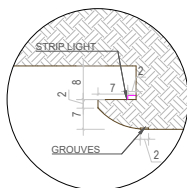

DETAIL 3

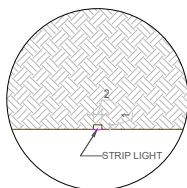

AREA DETAILS

FLOOR AREA : 190.26 SQM (2047.9 SQFT)
CARPET AREA : 169.86 SQM (1828.3 SQFT)
WALL : 23 CM

REVISIONS			
NO.	DATE	DESCRIPTION	CHK
NOTES :- * ALL MEASUREMENTS ARE IN CM UNLESS OTHERWISE SPECIFIED * DRAWINGS NOT TO BE SCALED * DRAWINGS TO BE READ IN CONJUNCTION AND RELEVANT ARCHITECTURAL DRAWINGS			

NOTES :			

PROJECT		TITLE	
GRAND OAK APARTMENT INTERIOR		REFLECTED CEILING PLAN	
INTERIOR DESIGNERS ARCHITECTURE NEXT		CLIENT HAZEEB_SHABNA	
STRUCTURAL CONSULTANTS		DWG NO. : 006	
MEP CONSULTANTS		LANDSCAPE	
THIS DRAWING IS COPYRIGHT PROTECTED, IT IS THE PROPERTY OF ARCHITECTURE NEXT. IT IS NOT TO BE REPRODUCED, COPIED, HANDED OVER TO A THIRD PARTY OR USED FOR ANY PURPOSE OTHER THAN THAT FOR WHICH IT HAS BEEN LOANED.		DRN. : KETH	
		DATE : 28.09.2025	
		CKD. : NAP	
		SCALE : NTS	

