


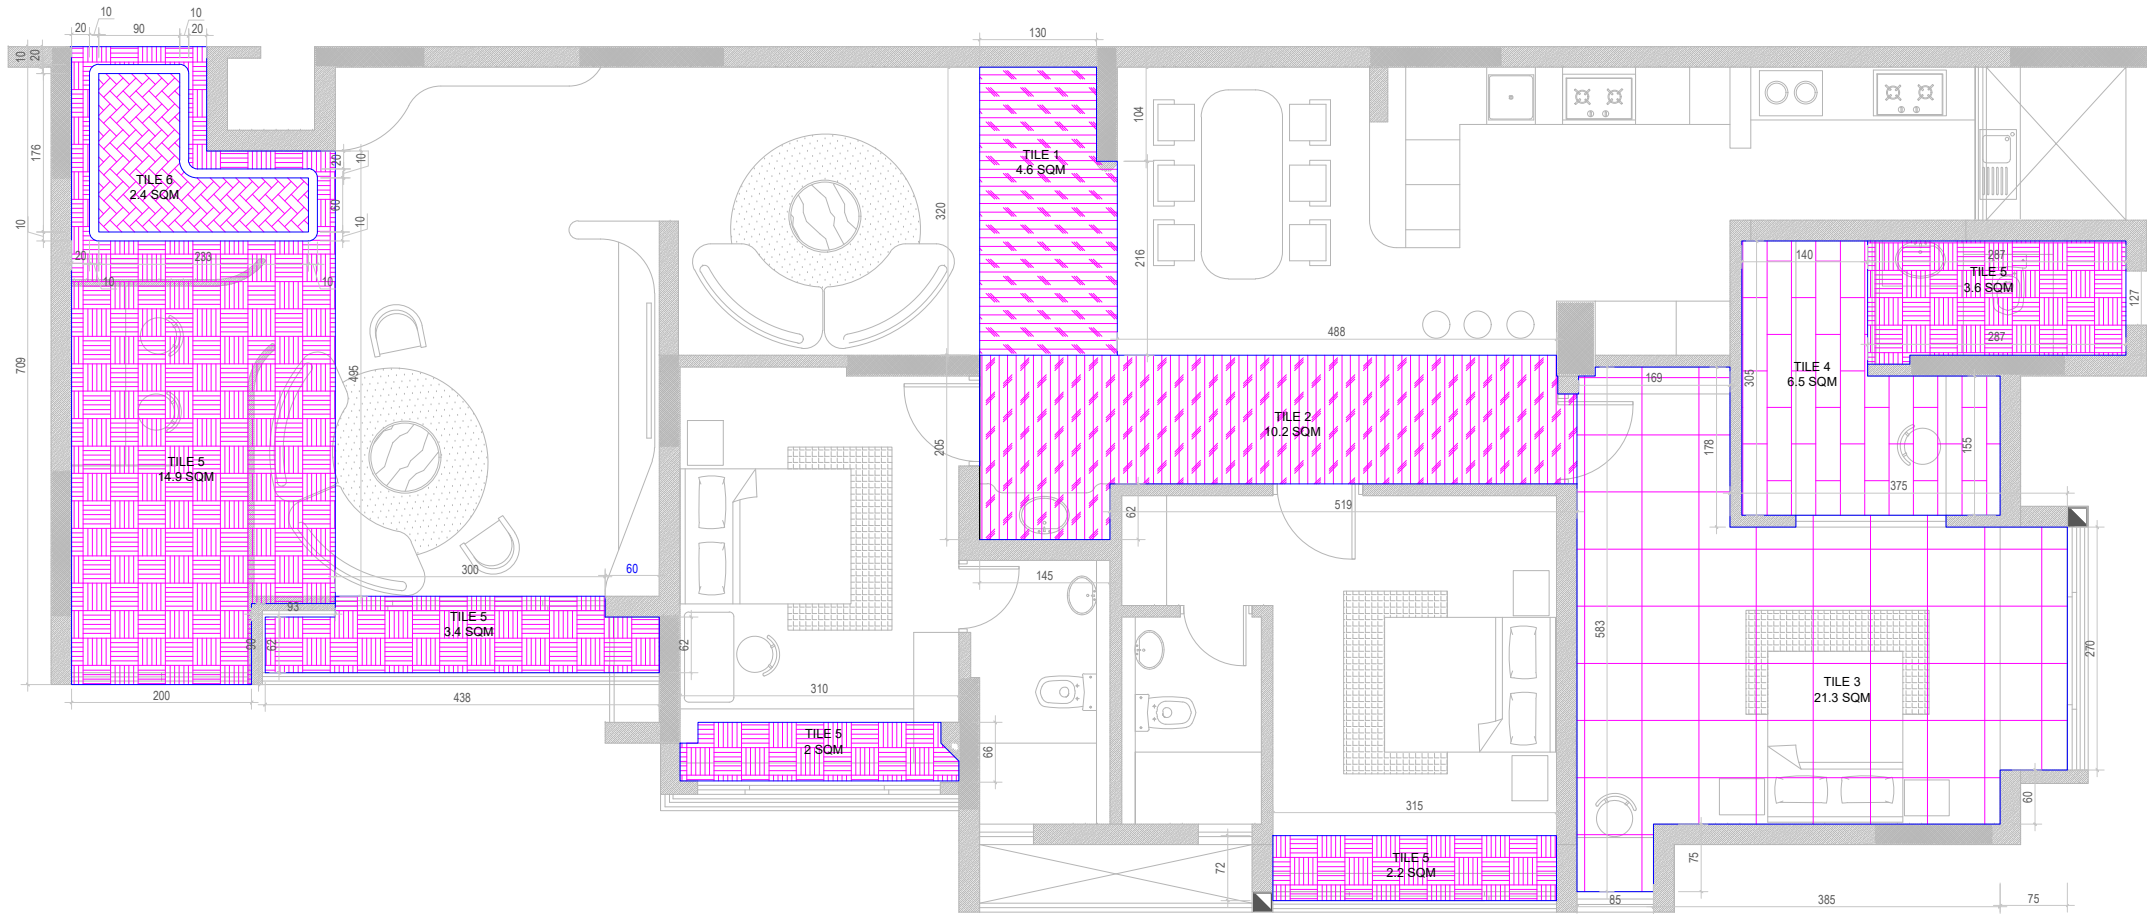

REVISIONS			
NO.	DATE	DESCRIPTION	CHK
NOTES :- * ALL MEASUREMENTS ARE IN CM UNLESS OTHERWISE SPECIFIED * DRAWINGS NOT TO BE SCALED * DRAWINGS TO BE READ IN CONJUNCTION AND RELEVANT ARCHITECTURAL DRAWINGS			

NOTES :

Architecture
Next

FIRST FLOOR | HILITE BUSINESS PARK | CALICUT | 9995145694

PROJECT

GRAND OAK APARTMENT INTERIOR

INTERIOR DESIGNERS

ARCHITECTURE NEXT

STRUCTURAL CONSULTANTS

MEP CONSULTANTS

THIS DRAWING IS COPYRIGHT PROTECTED, IT IS THE PROPERTY OF **ARCHITECTURE NEXT**. IT IS NOT TO BE REPRODUCED, COPIED, HANDED OVER TO A THIRD PARTY OR USED FOR ANY PURPOSE OTHER THAN THAT FOR WHICH IT HAS BEEN LOANED.

TITLE

TILE LAYOUT

CLIENT

HAZEEB_SHABNA

DWG NO. : 005

DRN. : KETH

CKD. : NAP

DATE : 08.11.2025

SCALE : NTS

N

Architecture
Next

+91 9995 1456 94