



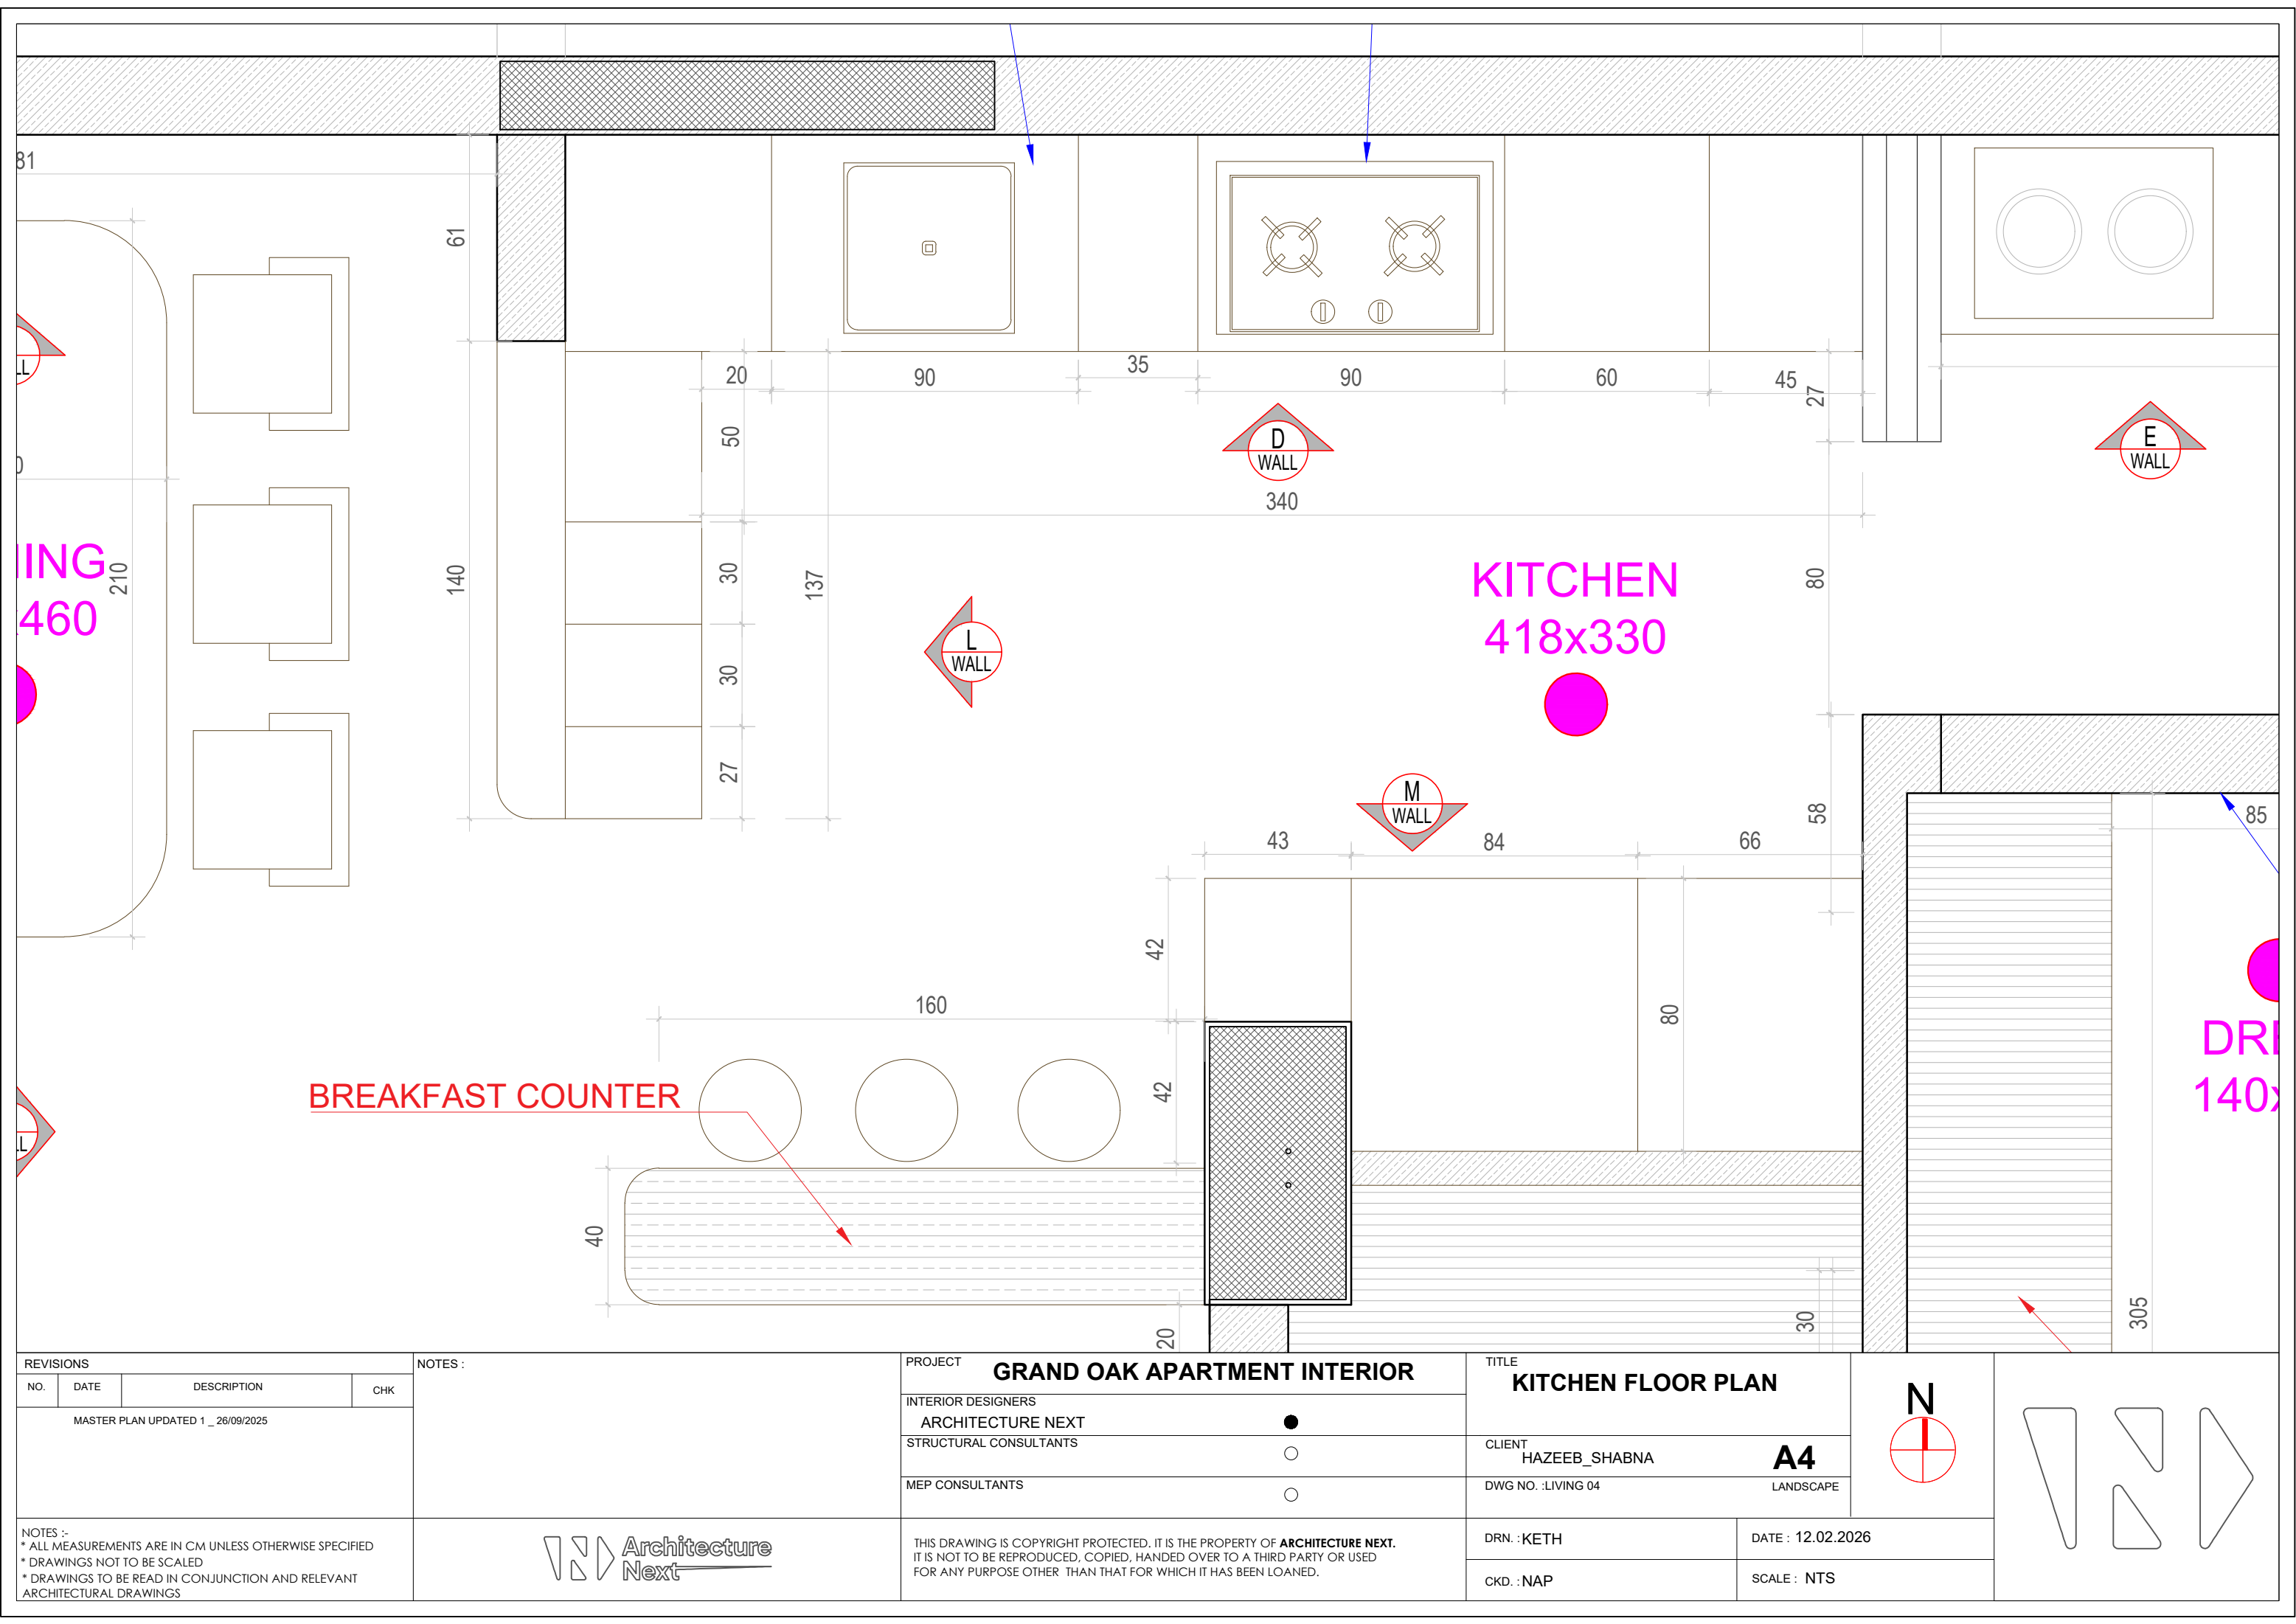

REVISIONS				NOTES :	PROJECT		TITLE		N		
NO.	DATE	DESCRIPTION	CHK		GRAND OAK APARTMENT INTERIOR		KITCHEN FLOOR PLAN				
MASTER PLAN UPDATED 1 _ 26/09/2025					INTERIOR DESIGNERS		CLIENT				
					ARCHITECTURE NEXT		HAZEEB_SHABNA				
					STRUCTURAL CONSULTANTS		DWG NO. :LIVING 04				
				MEP CONSULTANTS		LANDSCAPE					
NOTES :- * ALL MEASUREMENTS ARE IN CM UNLESS OTHERWISE SPECIFIED * DRAWINGS NOT TO BE SCALED * DRAWINGS TO BE READ IN CONJUNCTION AND RELEVANT ARCHITECTURAL DRAWINGS				Architecture Next		THIS DRAWING IS COPYRIGHT PROTECTED. IT IS THE PROPERTY OF ARCHITECTURE NEXT . IT IS NOT TO BE REPRODUCED, COPIED, HANDED OVER TO A THIRD PARTY OR USED FOR ANY PURPOSE OTHER THAN THAT FOR WHICH IT HAS BEEN LOANED.		DRN. :KETH		DATE : 12.02.2026	
								CKD. :NAP		SCALE : NTS	

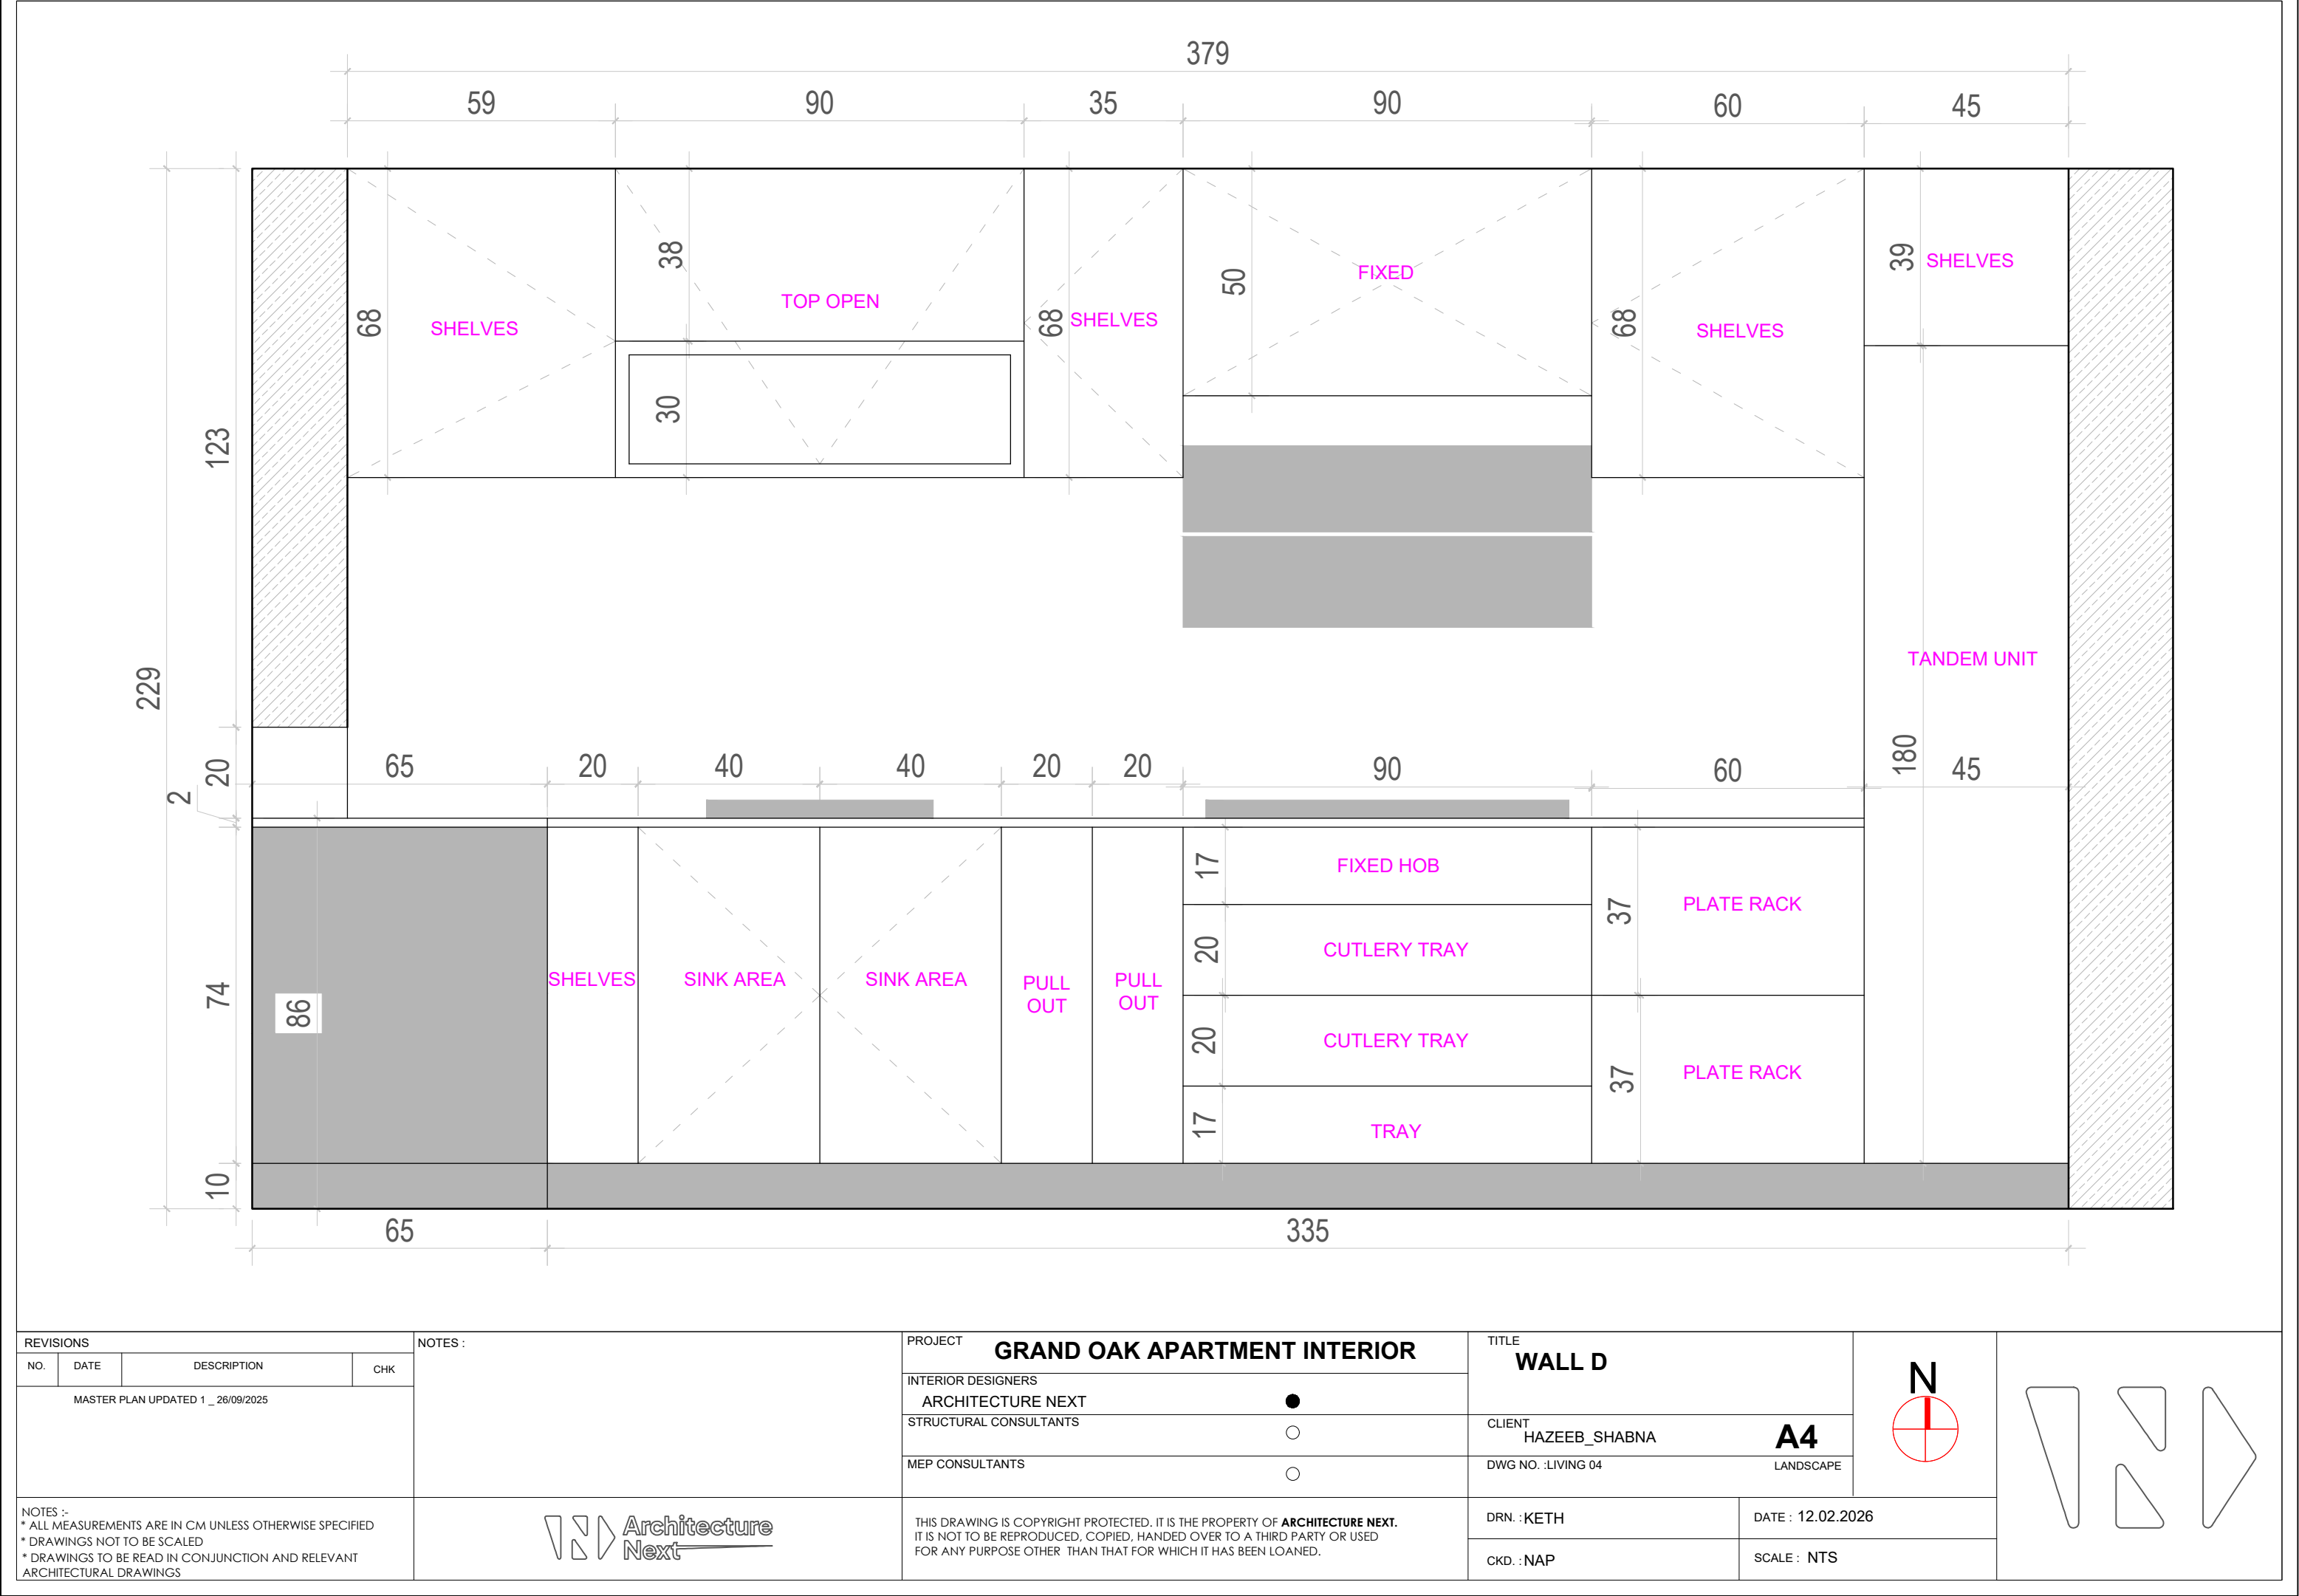

REVISIONS				NOTES :	Architecture Next	PROJECT		TITLE		N	
NO.	DATE	DESCRIPTION	CHK			GRAND OAK APARTMENT INTERIOR		WALL D			
MASTER PLAN UPDATED 1 _ 26/09/2025						INTERIOR DESIGNERS		CLIENT			
						ARCHITECTURE NEXT		HAZEEB_SHABNA			
				STRUCTURAL CONSULTANTS		DWG NO. :LIVING 04		LANDSCAPE			
				MEP CONSULTANTS							
NOTES :- * ALL MEASUREMENTS ARE IN CM UNLESS OTHERWISE SPECIFIED * DRAWINGS NOT TO BE SCALED * DRAWINGS TO BE READ IN CONJUNCTION AND RELEVANT ARCHITECTURAL DRAWINGS						THIS DRAWING IS COPYRIGHT PROTECTED. IT IS THE PROPERTY OF ARCHITECTURE NEXT . IT IS NOT TO BE REPRODUCED, COPIED, HANDED OVER TO A THIRD PARTY OR USED FOR ANY PURPOSE OTHER THAN THAT FOR WHICH IT HAS BEEN LOANED.		DRN. :KETH		DATE : 12.02.2026	
								CKD. :NAP		SCALE : NTS	

A KITCHEN ACCESSORIES			
Sl. #.	PARTICULARS	IMAGE	DESCRIPTION
A1	Glass & Plate Tray		Hettich - 9206161 Cargo dish drainer set - 900 mm (MRP: Rs. 7275/-)
A2	Cutlery Tray		Olive - 5610050090 620-850 x 523 x 55 mm (MRP: Rs. 2835/-)
A3	Plate Rack		Olive - 561 003 555 0 525 mm Length (MRP: Rs. 526/-)
A4	Saucer Rack		Olive - 561 004 555 0 525 mm Length (MRP: Rs. 525/-)
A5	Spice Pull out		Olive Smartek - 561 001 043 0 300 mm Length (MRP: Rs. 11,790/-)
A6	Corner Unit		Olive Smartek - 27700 Show & Corner 815 x 400 x (600-700) mm (MRP: Rs. 22,400/-)

A7	Waste bin		Olive - Waste bin 6 (Revolving) 270 x 335 mm (MRP: Rs. 2580/-)
A8	Tandem Unit		Olive - 101 024 012 0 Tandem Pantry Unit Smartek Series (Grey - Glass) 380 x 510 x 1820 mm (MRP: Rs. 25,300/-)
A9	Anti skid Mat		Olive - Anti skid mat 20 m roll (MRP: Rs. 6,900/-)

REVISIONS				NOTES :	PROJECT	TITLE				
NO.	DATE	DESCRIPTION	CHK		GRAND OAK APARTMENT INTERIOR	KITCHEN ACCESSORIES				
MASTER PLAN UPDATED 1 _ 26/09/2025					INTERIOR DESIGNERS ARCHITECTURE NEXT	●	CLIENT HAZEEB_SHABNA			A4
					STRUCTURAL CONSULTANTS	○	DWG NO. :LIVING 04			LANDSCAPE
NOTES :- * ALL MEASUREMENTS ARE IN CM UNLESS OTHERWISE SPECIFIED * DRAWINGS NOT TO BE SCALED * DRAWINGS TO BE READ IN CONJUNCTION AND RELEVANT ARCHITECTURAL DRAWINGS				MEP CONSULTANTS	○	DRN. : KETH		DATE : 12.02.2026		
				THIS DRAWING IS COPYRIGHT PROTECTED. IT IS THE PROPERTY OF ARCHITECTURE NEXT. IT IS NOT TO BE REPRODUCED, COPIED, HANDED OVER TO A THIRD PARTY OR USED FOR ANY PURPOSE OTHER THAN THAT FOR WHICH IT HAS BEEN LOANED.				CKD. : NAP		SCALE : NTS